LEGEND

SL	FIRE ALARM SOUNDER WITH STROBE LIGHT
FATB	FIRE ALARM TERMINAL BOX
SD A	ADDRESSABLE SMOKE DETECTOR
HD A	ADDRESSABLE HEAT DETECTOR
F	FIREMAN'S TELEPHONE OUTLET
A	ANNUNCIATOR
C	CONTROL MODULE
M	MONITOR MODULE
FS	FLOW SWITCH
SS	SUPERVISORY SWITCH
F	ADDRESSABLE MANUAL PULL STATION

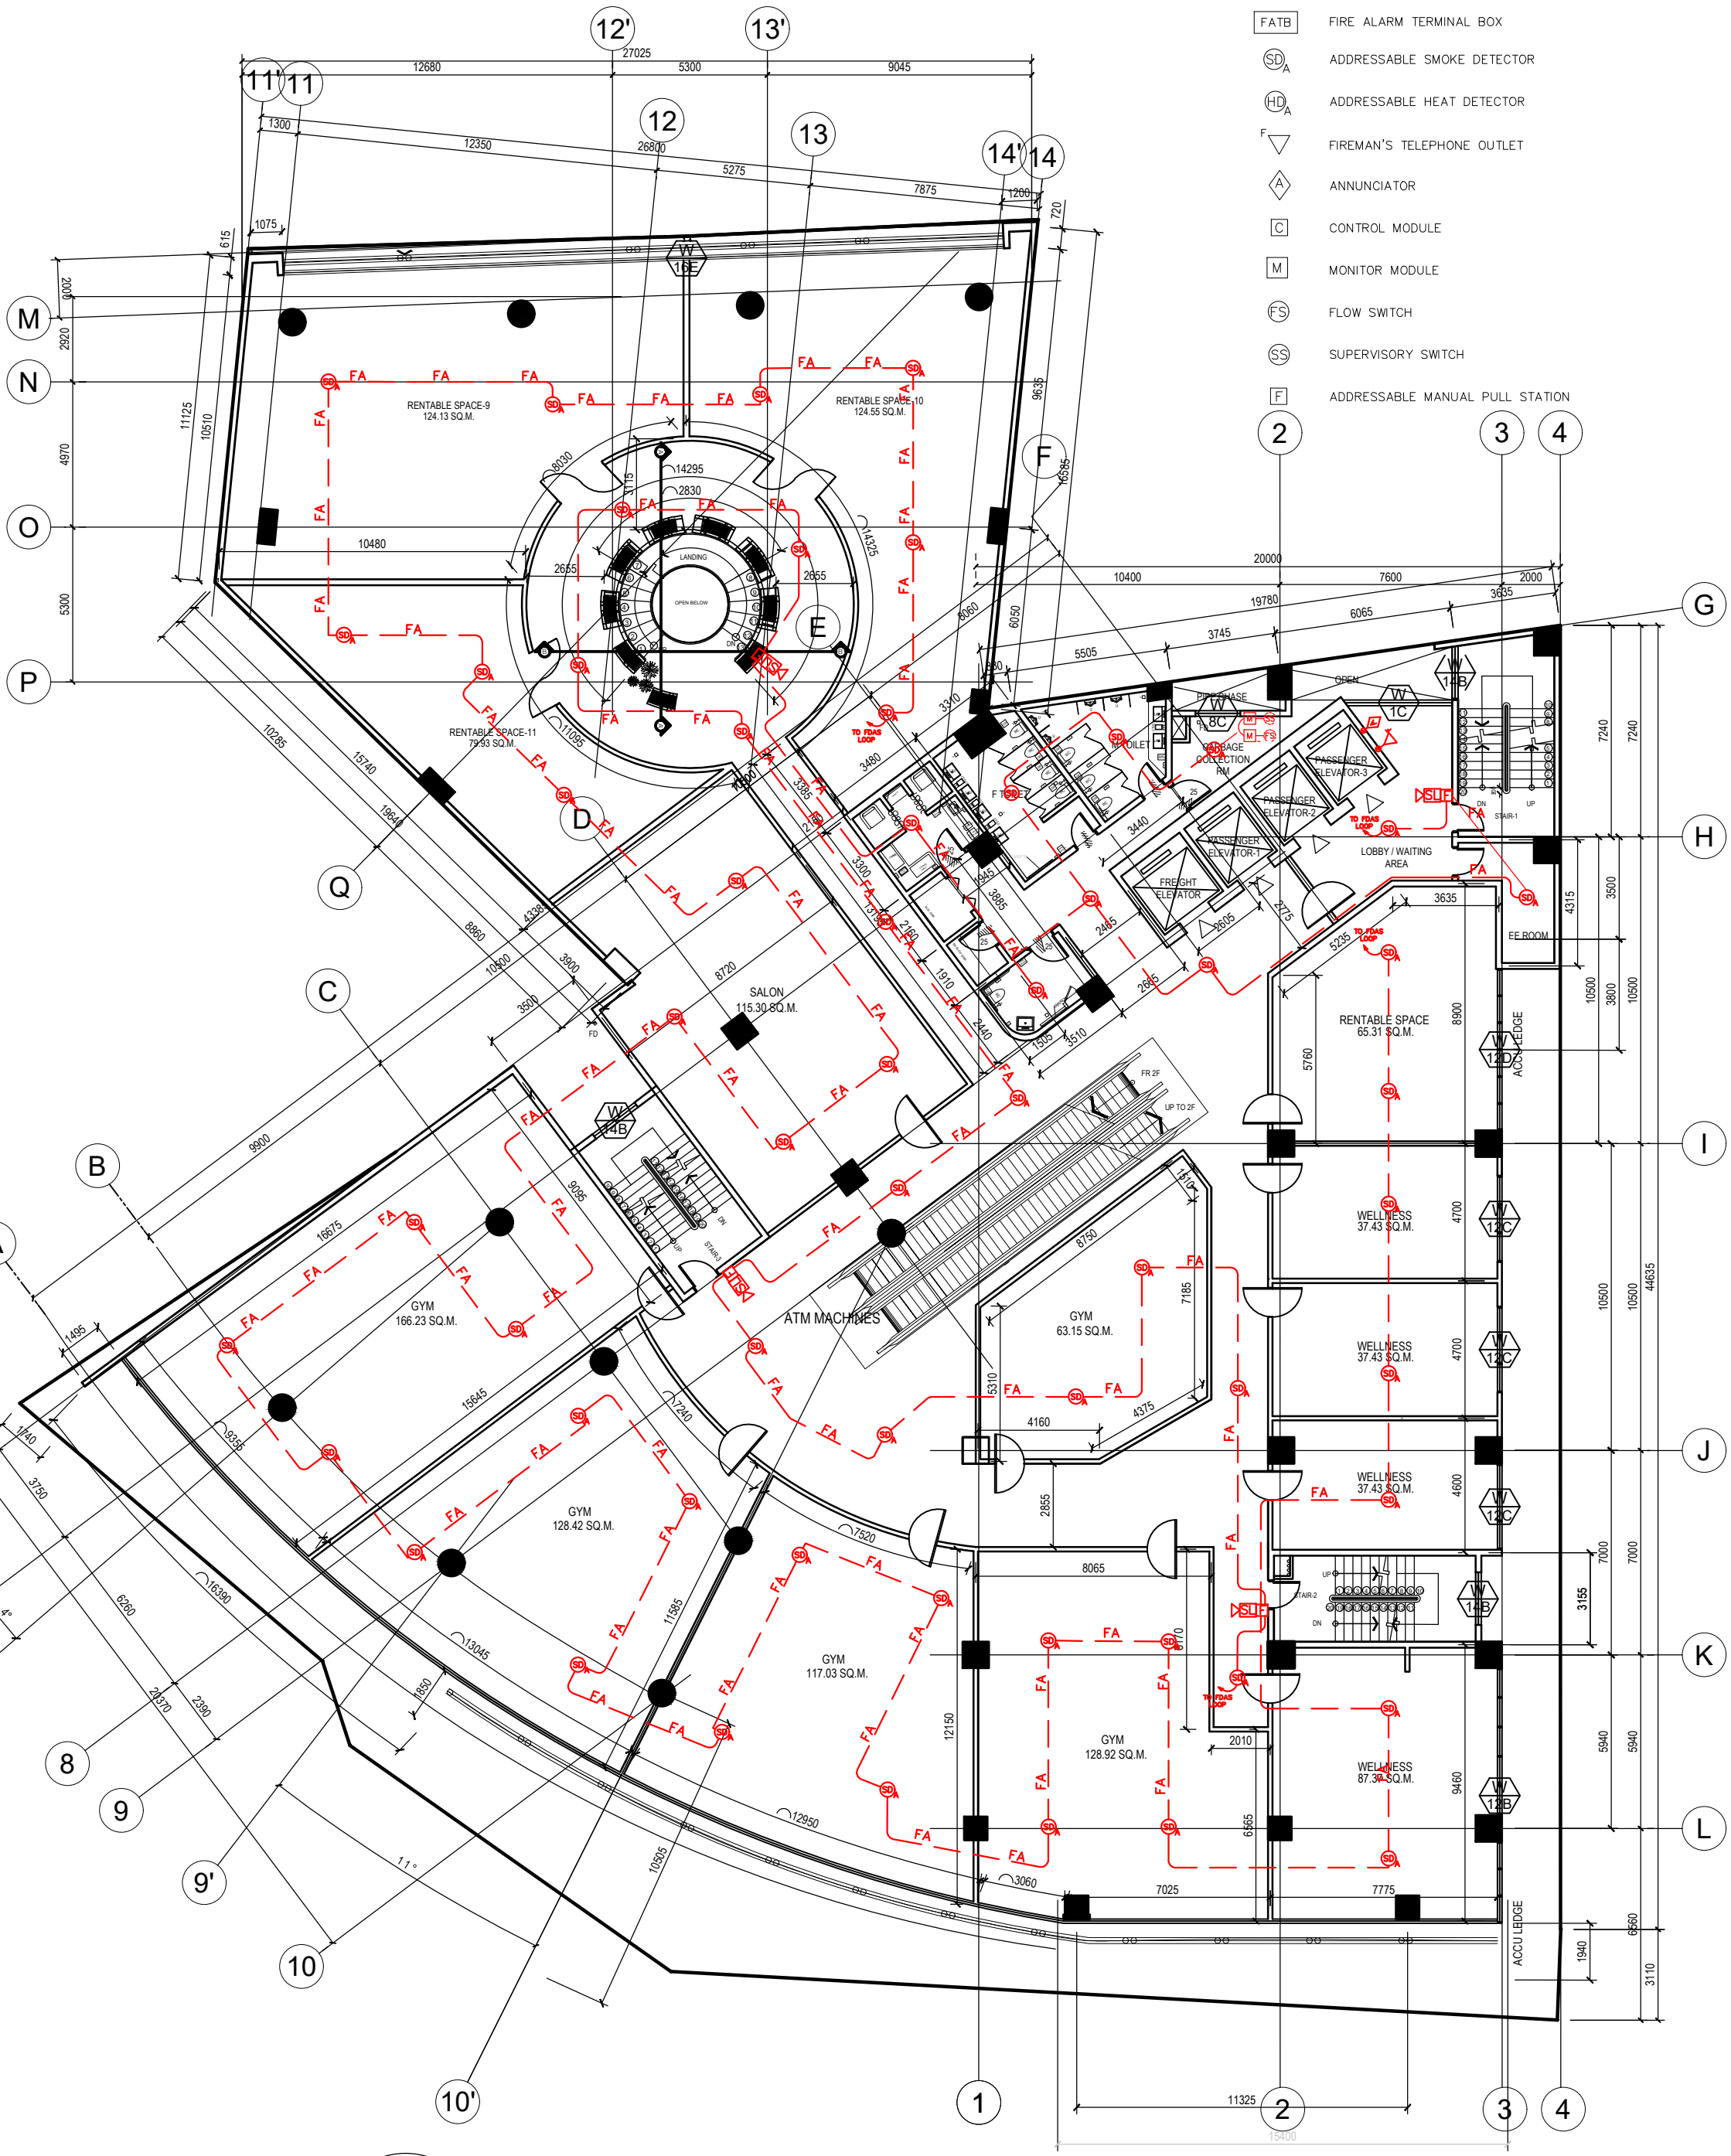

1 SECOND FLOOR FDAS LAYOUT

08

SCALE 1:200M

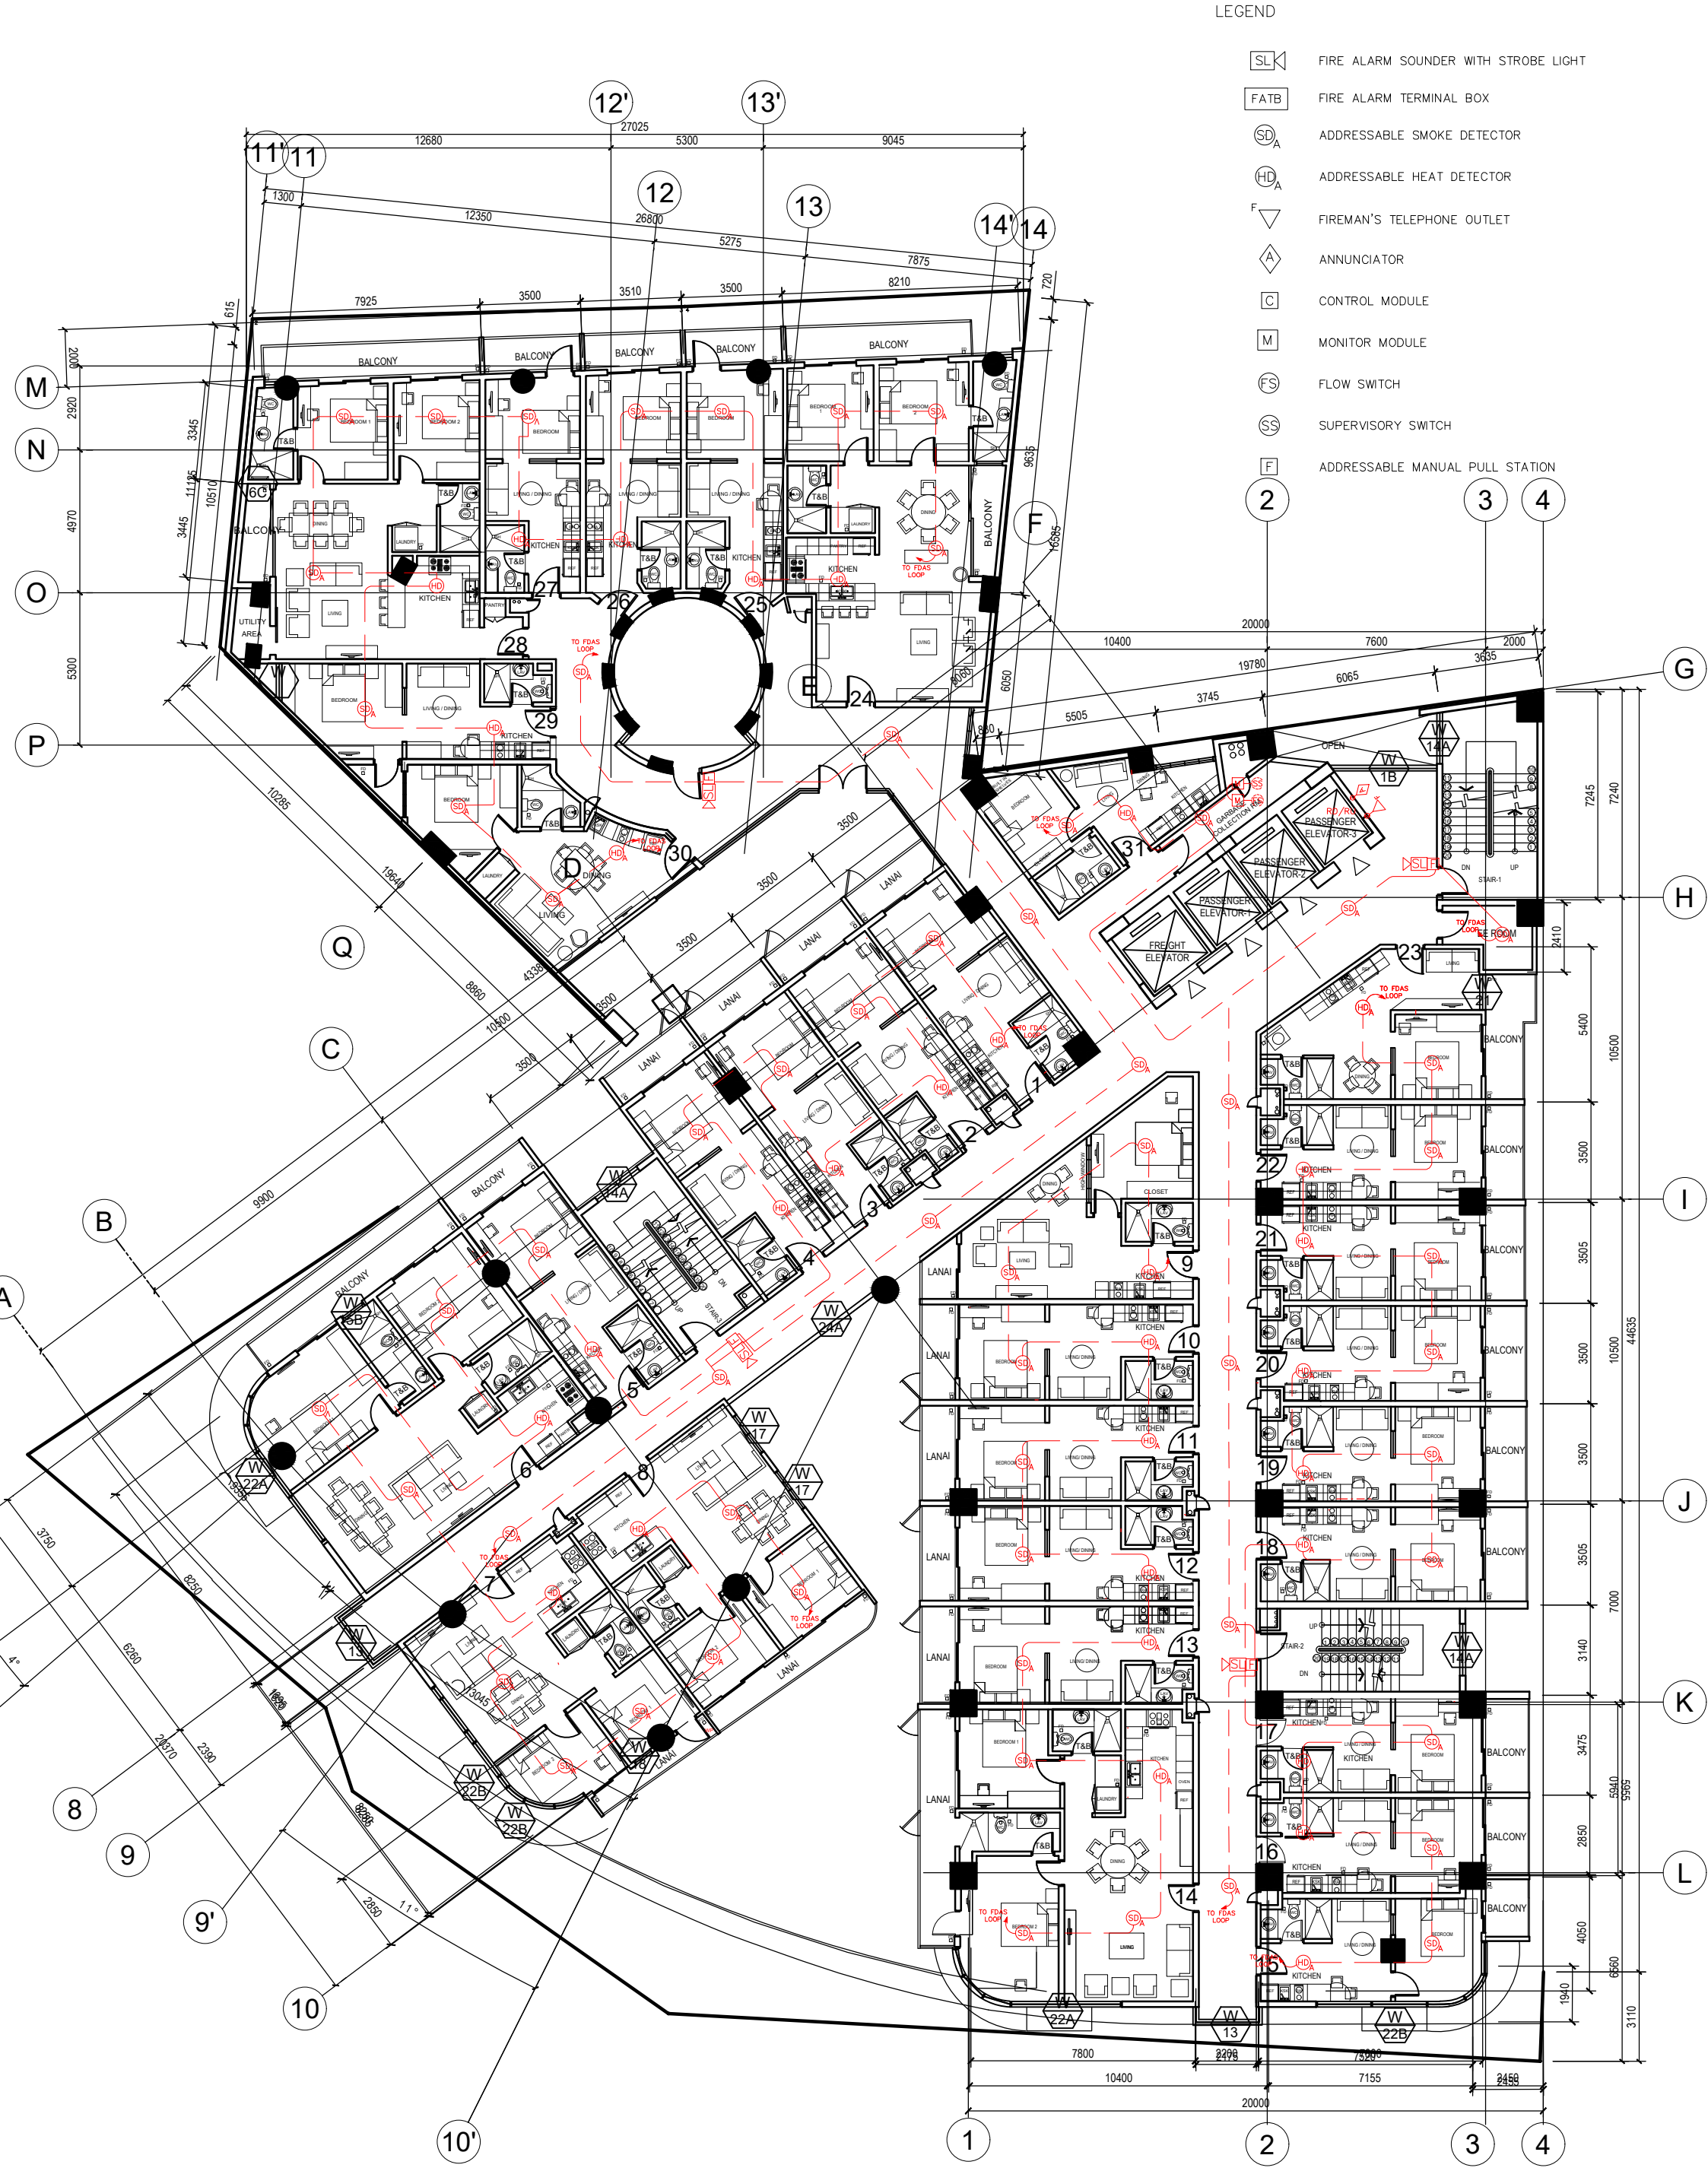

1 THIRD FLOOR FDAS LAYOUT

09

SCALE 1:200M

LEGEND

SL	FIRE ALARM SOUNDER WITH STROBE LIGHT
FATB	FIRE ALARM TERMINAL BOX
SD A	ADDRESSABLE SMOKE DETECTOR
HD A	ADDRESSABLE HEAT DETECTOR
F	FIREMAN'S TELEPHONE OUTLET
A	ANNUNCIATOR
C	CONTROL MODULE
M	MONITOR MODULE
FS	FLOW SWITCH
SS	SUPERVISORY SWITCH
F	ADDRESSABLE MANUAL PULL STATION

1 FOURTH FLOOR FDAS LAYOUT

10

SCALE **1:200M**

LEGEND

SL	FIRE ALARM SOUNDER WITH STROBE LIGHT
FATB	FIRE ALARM TERMINAL BOX
SD A	ADDRESSABLE SMOKE DETECTOR
HD A	ADDRESSABLE HEAT DETECTOR
F	FIREMAN'S TELEPHONE OUTLET
A	ANNUNCIATOR
C	CONTROL MODULE
M	MONITOR MODULE
FS	FLOW SWITCH
SS	SUPERVISORY SWITCH
F	ADDRESSABLE MANUAL PULL STATION

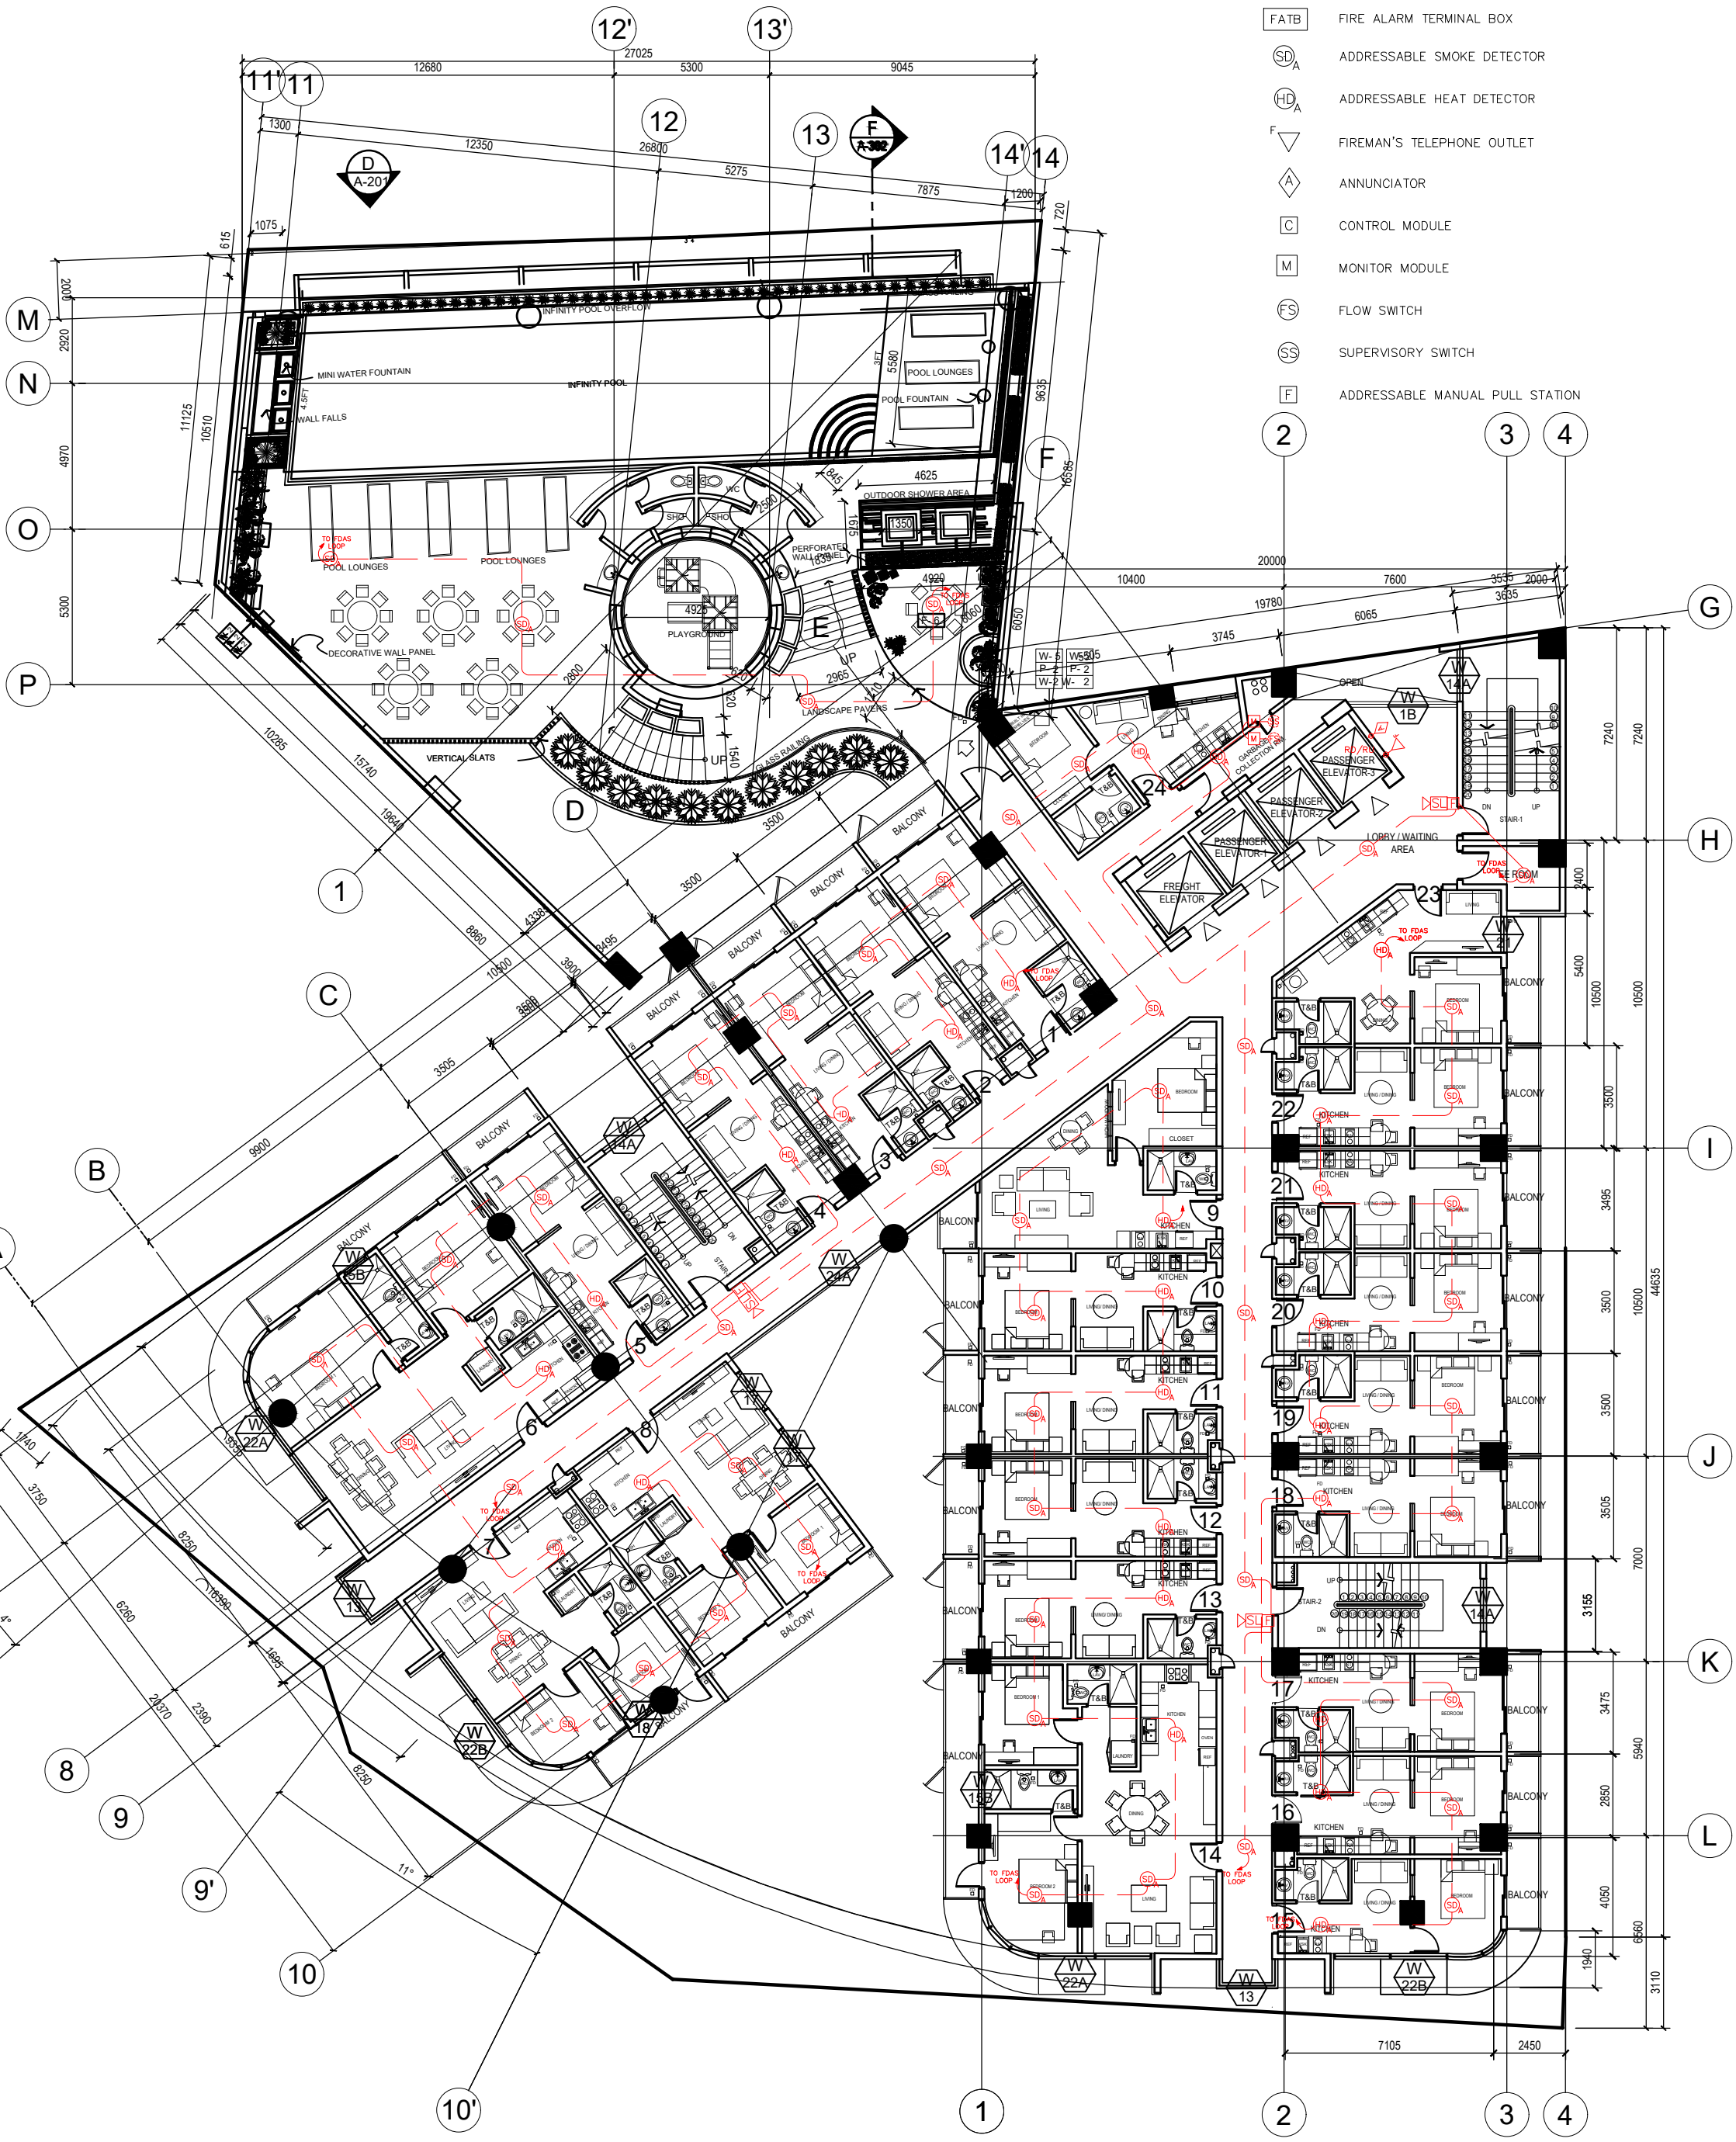

1 FIFTH FLOOR FDAS LAYOUT

11

SCALE 1:200M

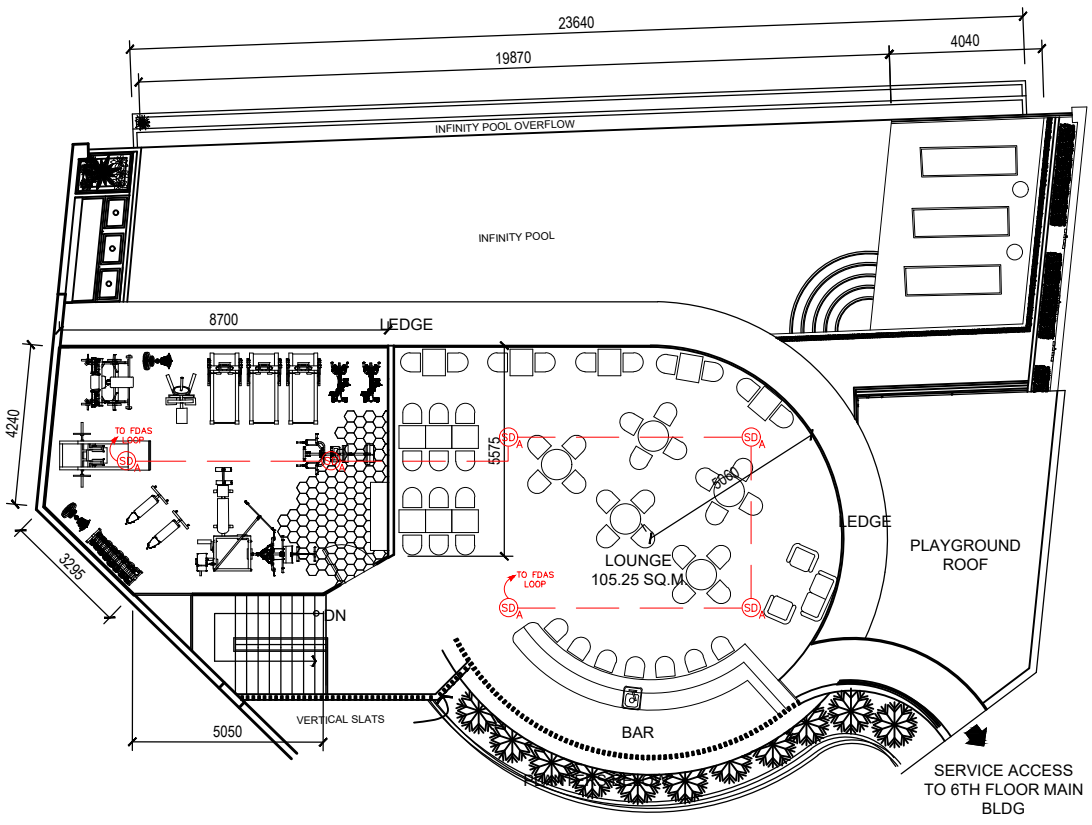

2
11

FIFTH FLOOR FDAS MEZZANINE

SCALE **1:200M**

LEGEND

SL	FIRE ALARM SOUNDER WITH STROBE LIGHT
FATB	FIRE ALARM TERMINAL BOX
SD A	ADDRESSABLE SMOKE DETECTOR
HD A	ADDRESSABLE HEAT DETECTOR
F	FIREMAN'S TELEPHONE OUTLET
A	ANNUNCIATOR
C	CONTROL MODULE
M	MONITOR MODULE
FS	FLOW SWITCH
SS	SUPERVISORY SWITCH
F	ADDRESSABLE MANUAL PULL STATION

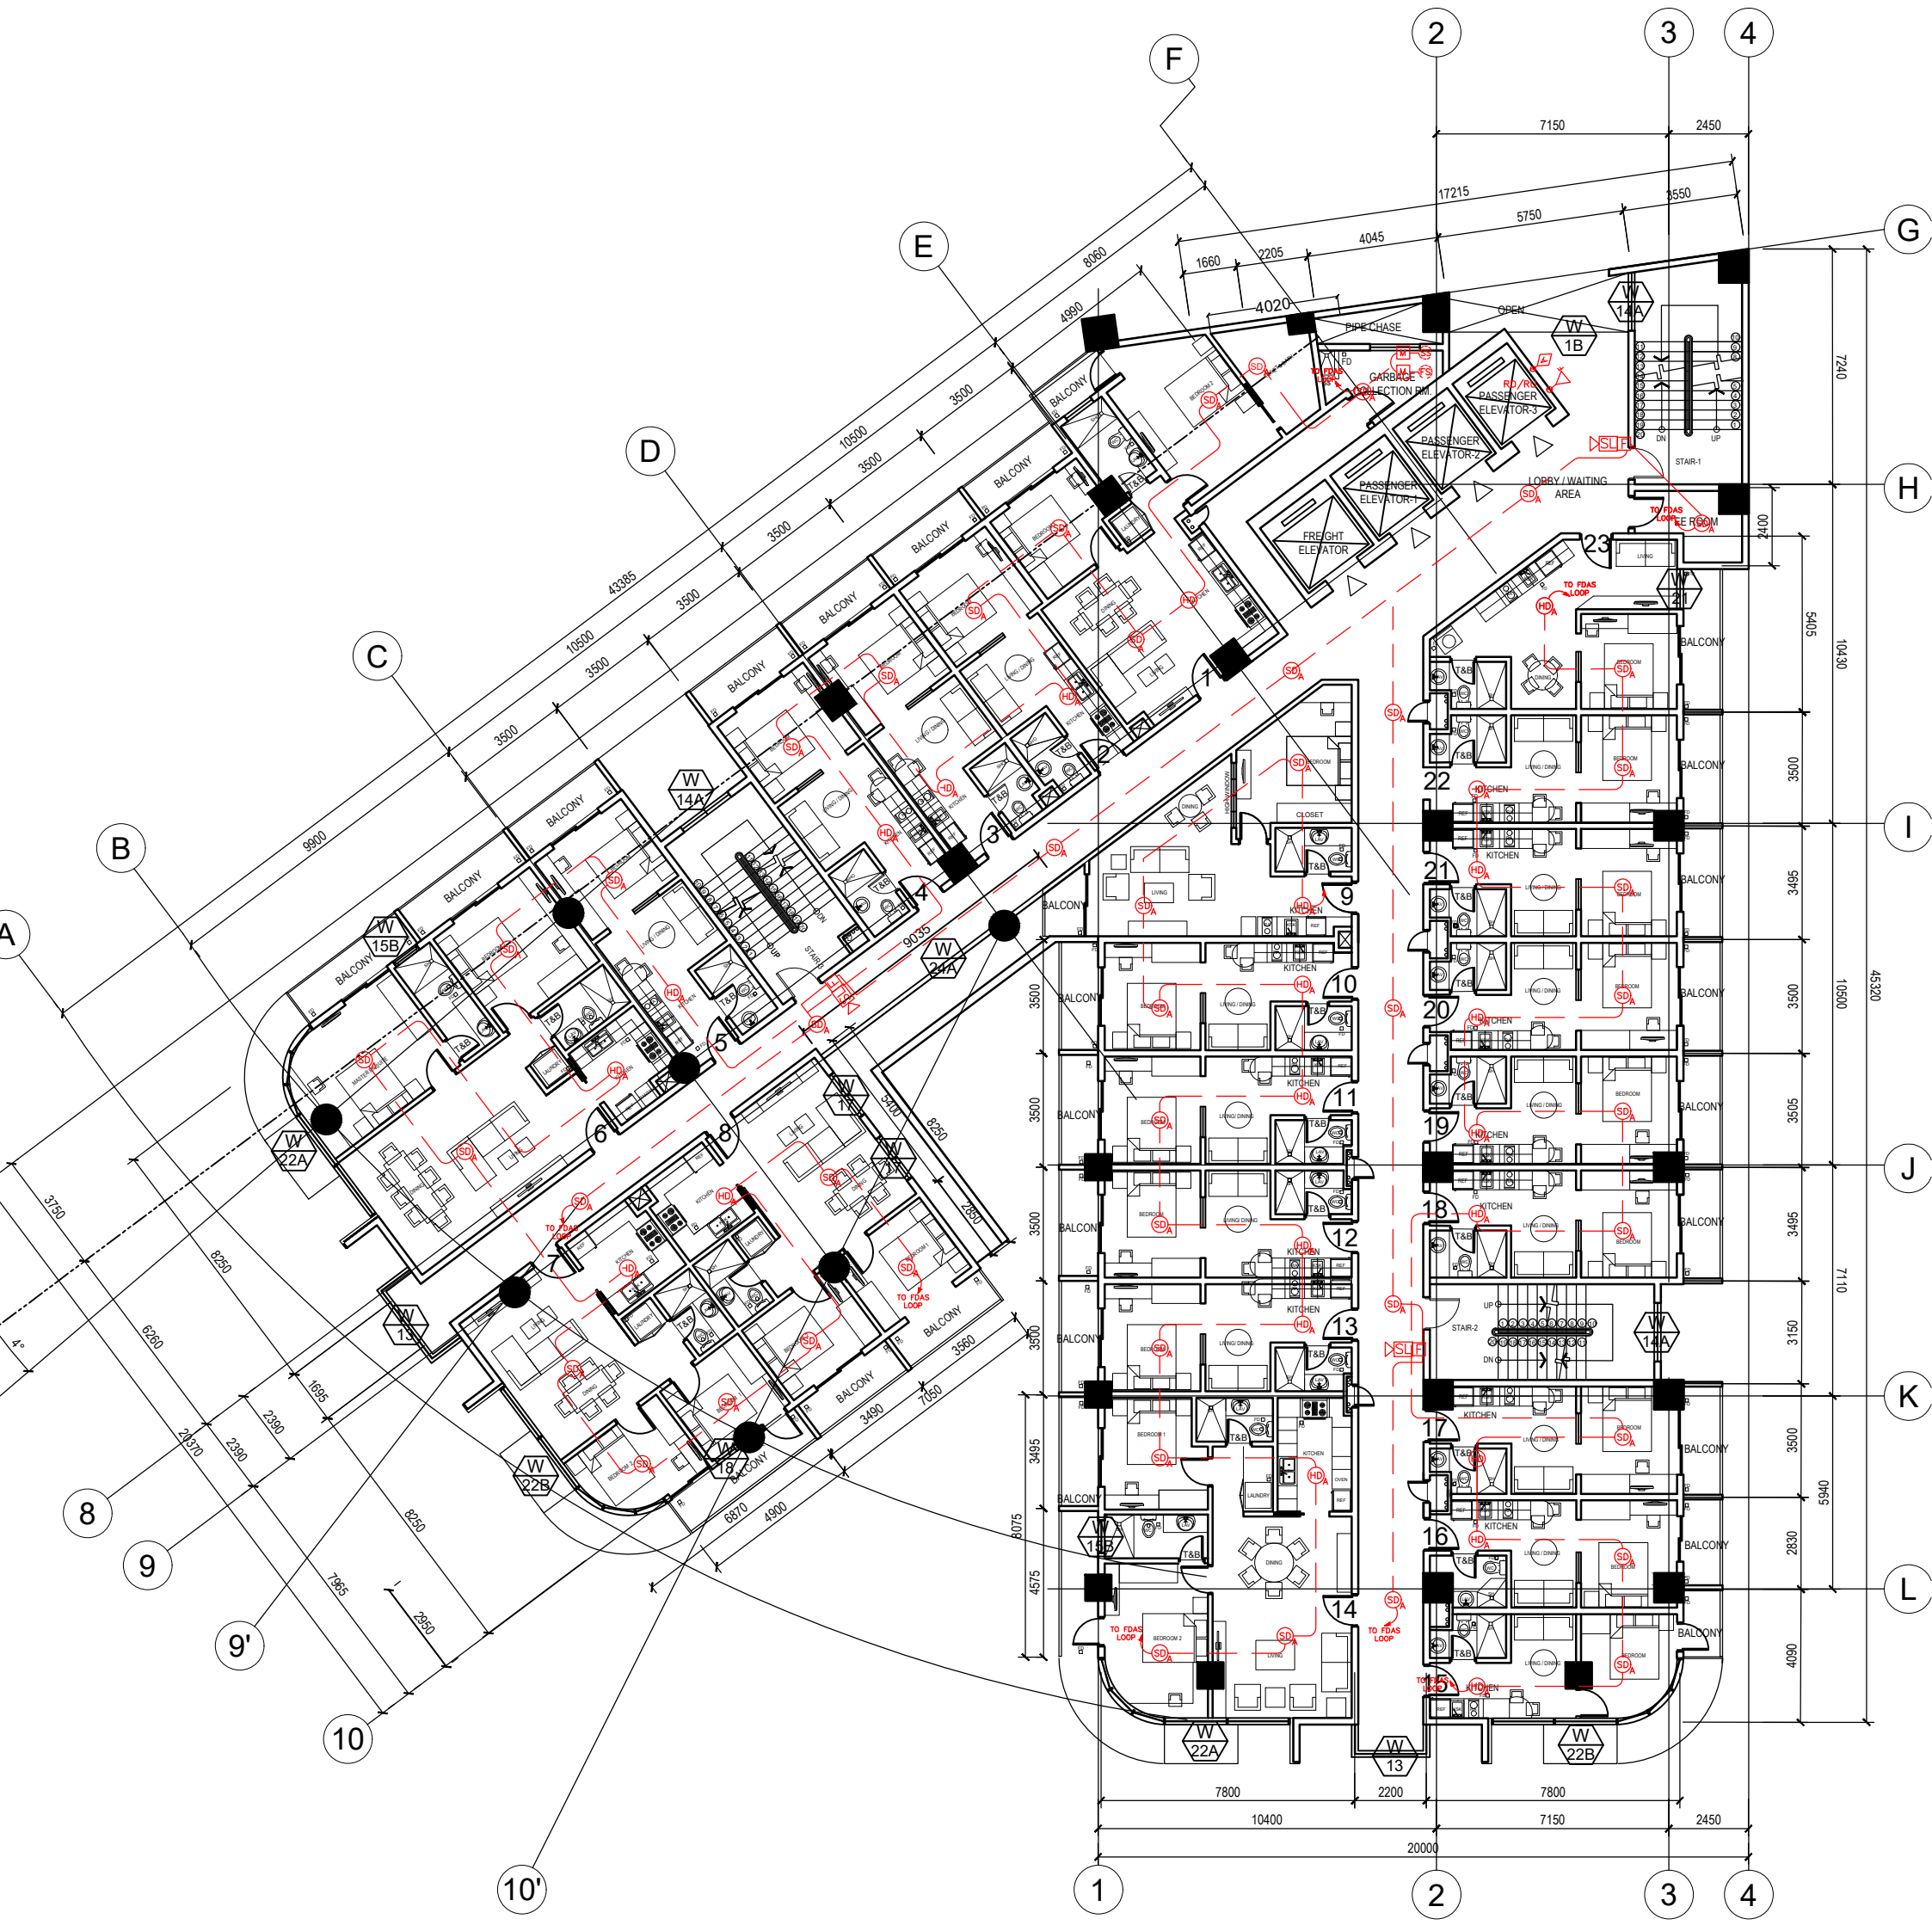

1 SIXTH TO EIGHTH FLOOR FDAS LAYOUT

12

SCALE **1:200M**

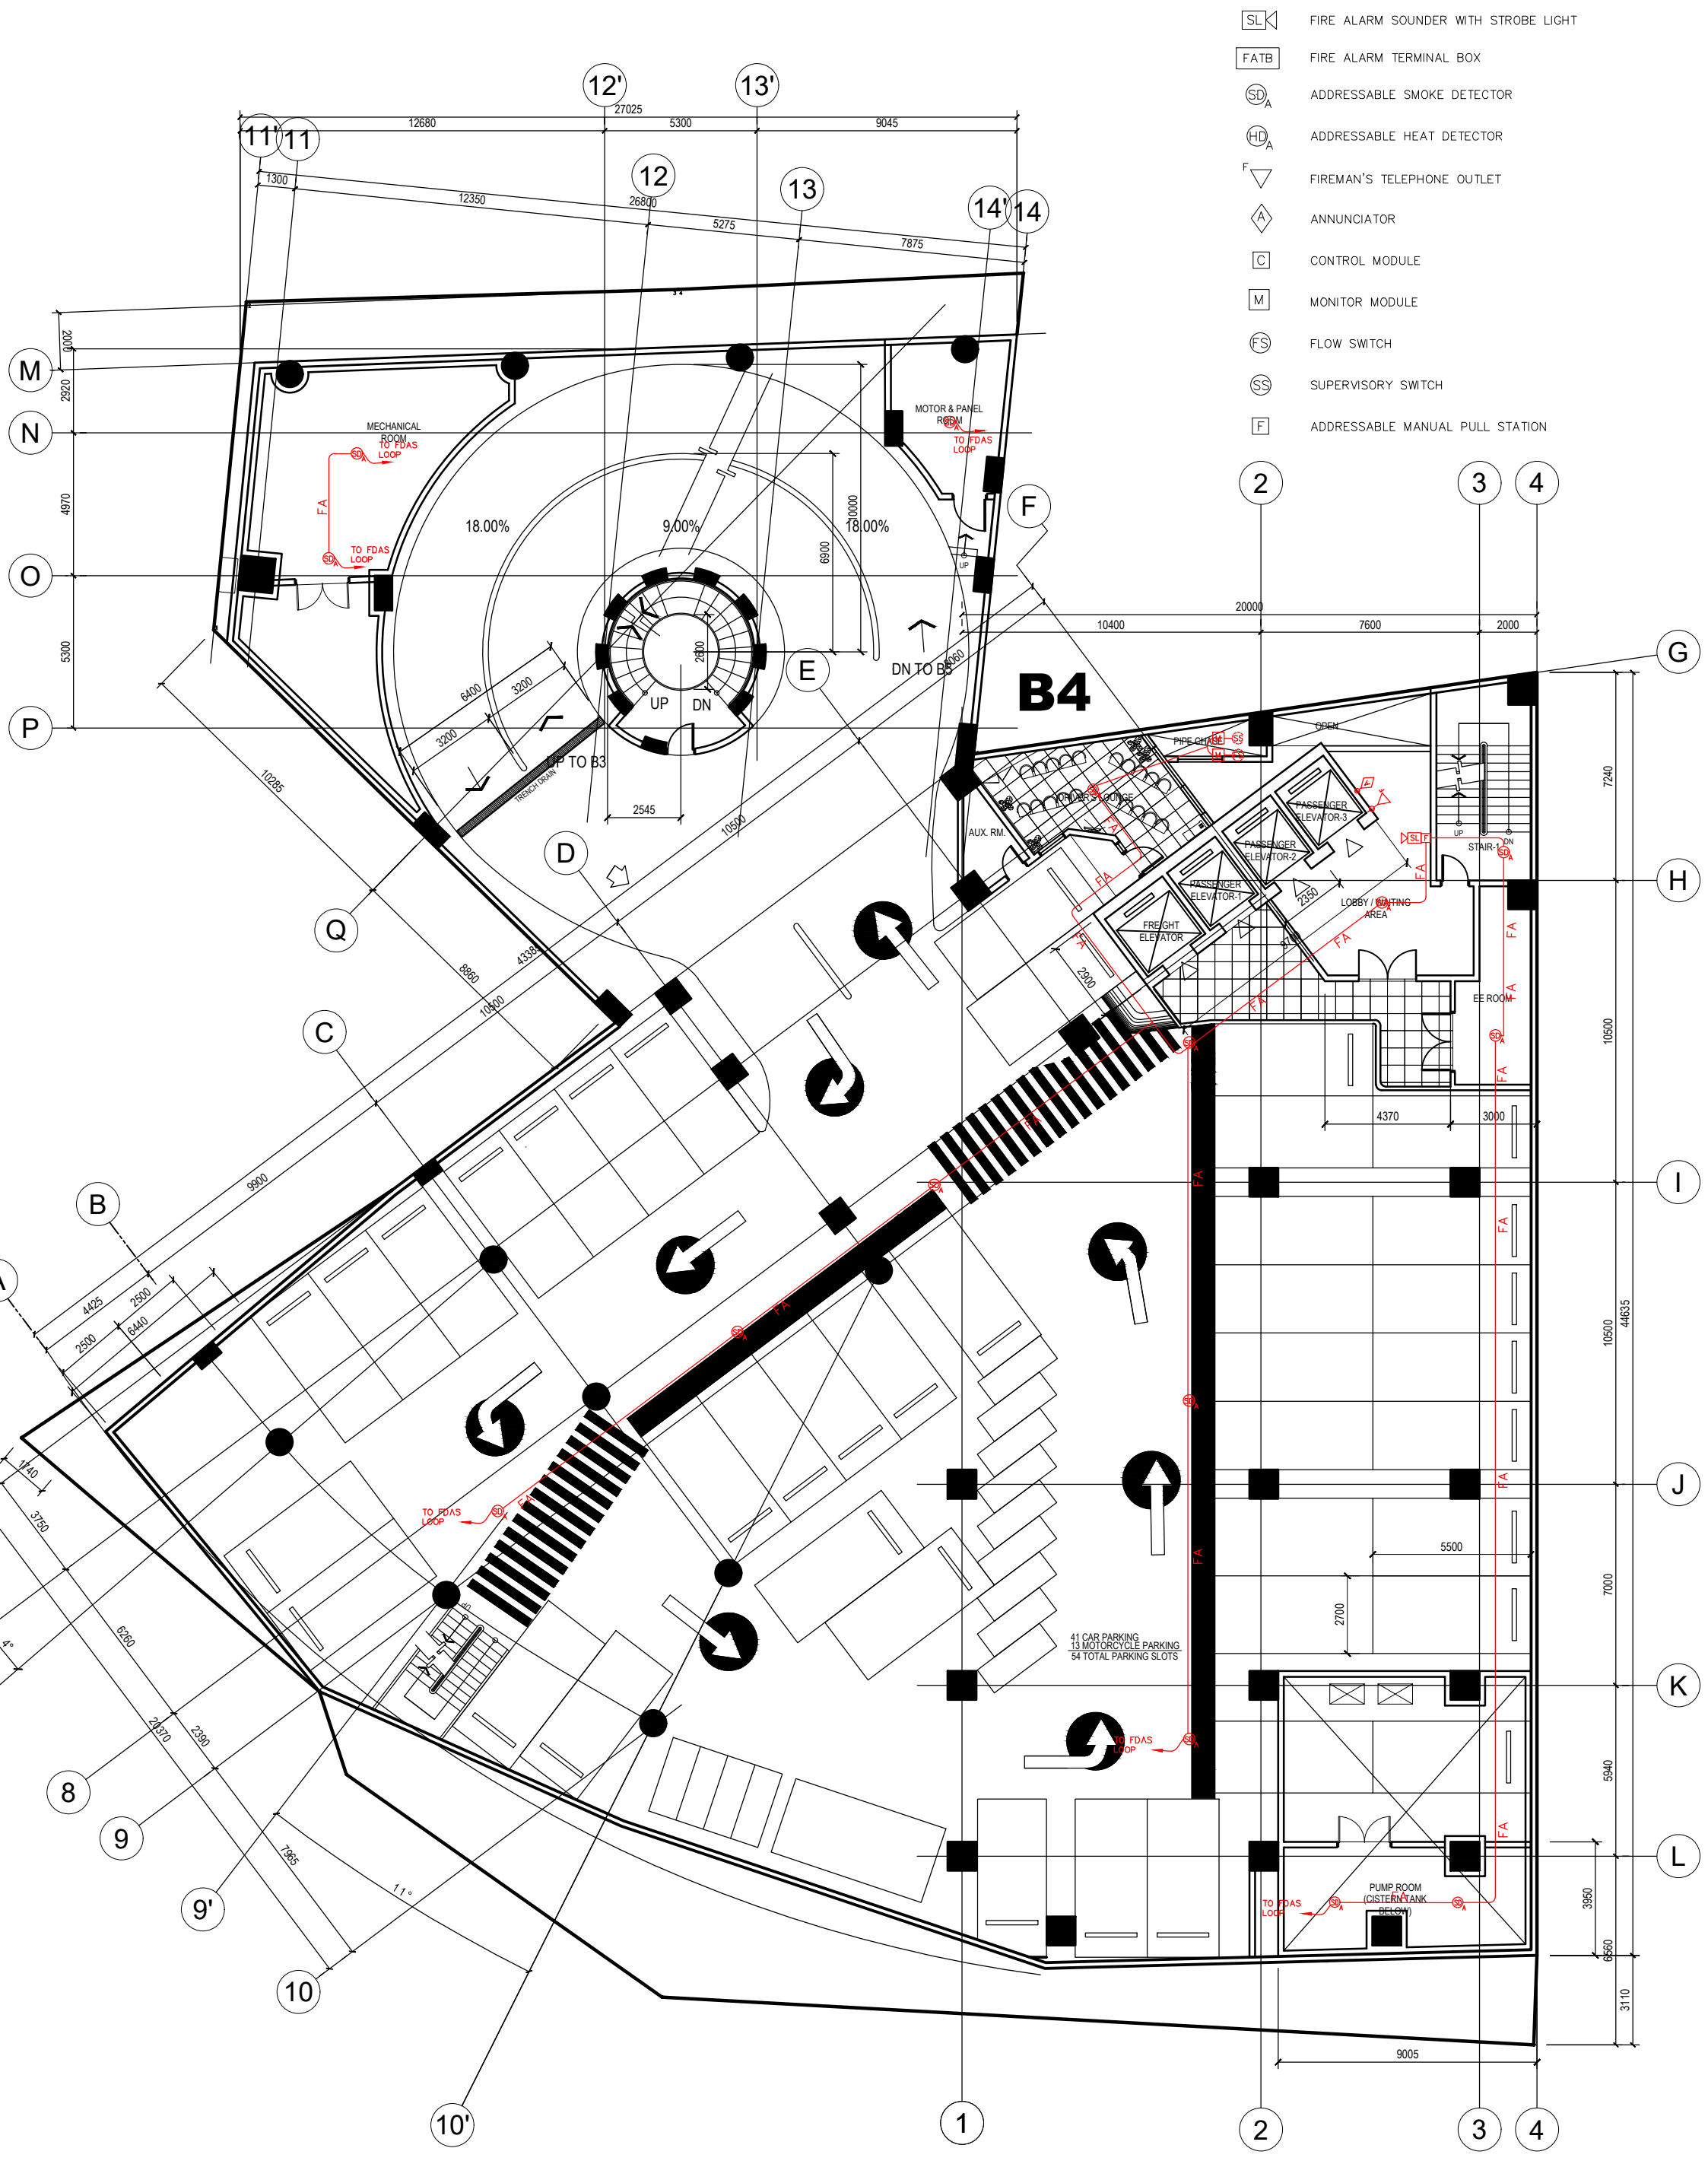

1 BASEMENT 1 FDAS LAYOUT

02

SCALE 1:200M

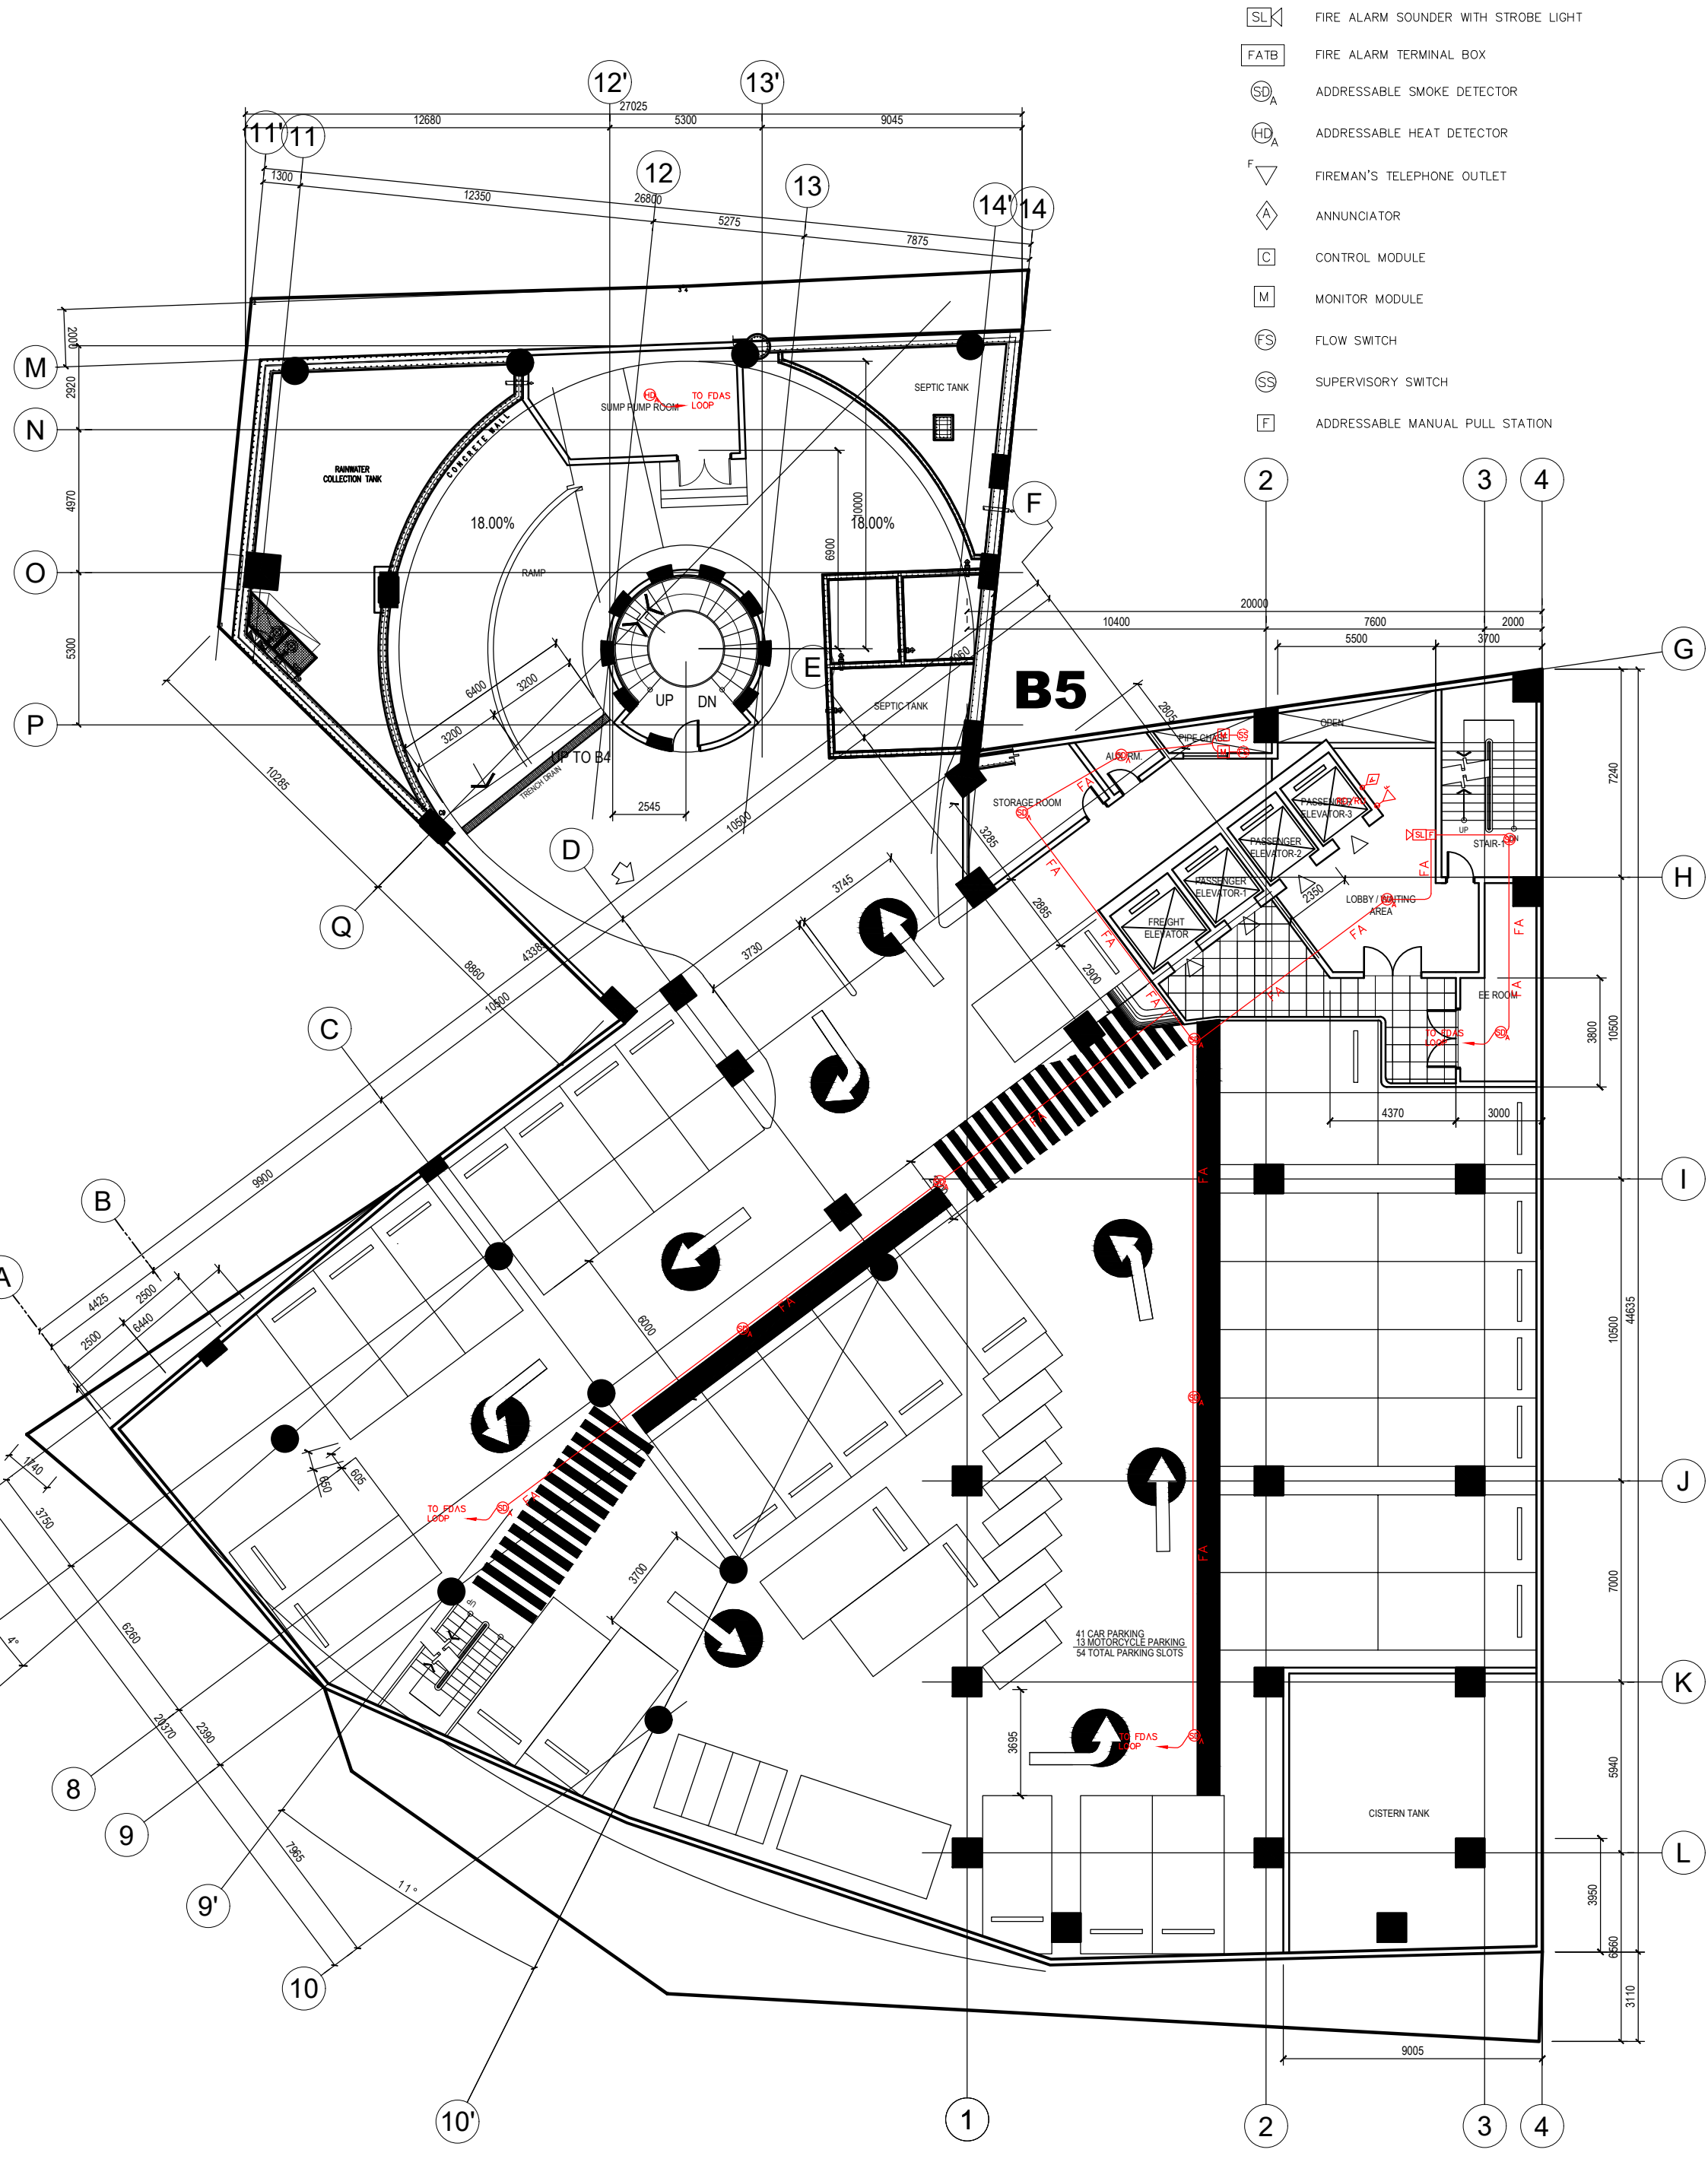

1 BASEMENT 2 FDAS LAYOUT

01

SCALE 1:200M

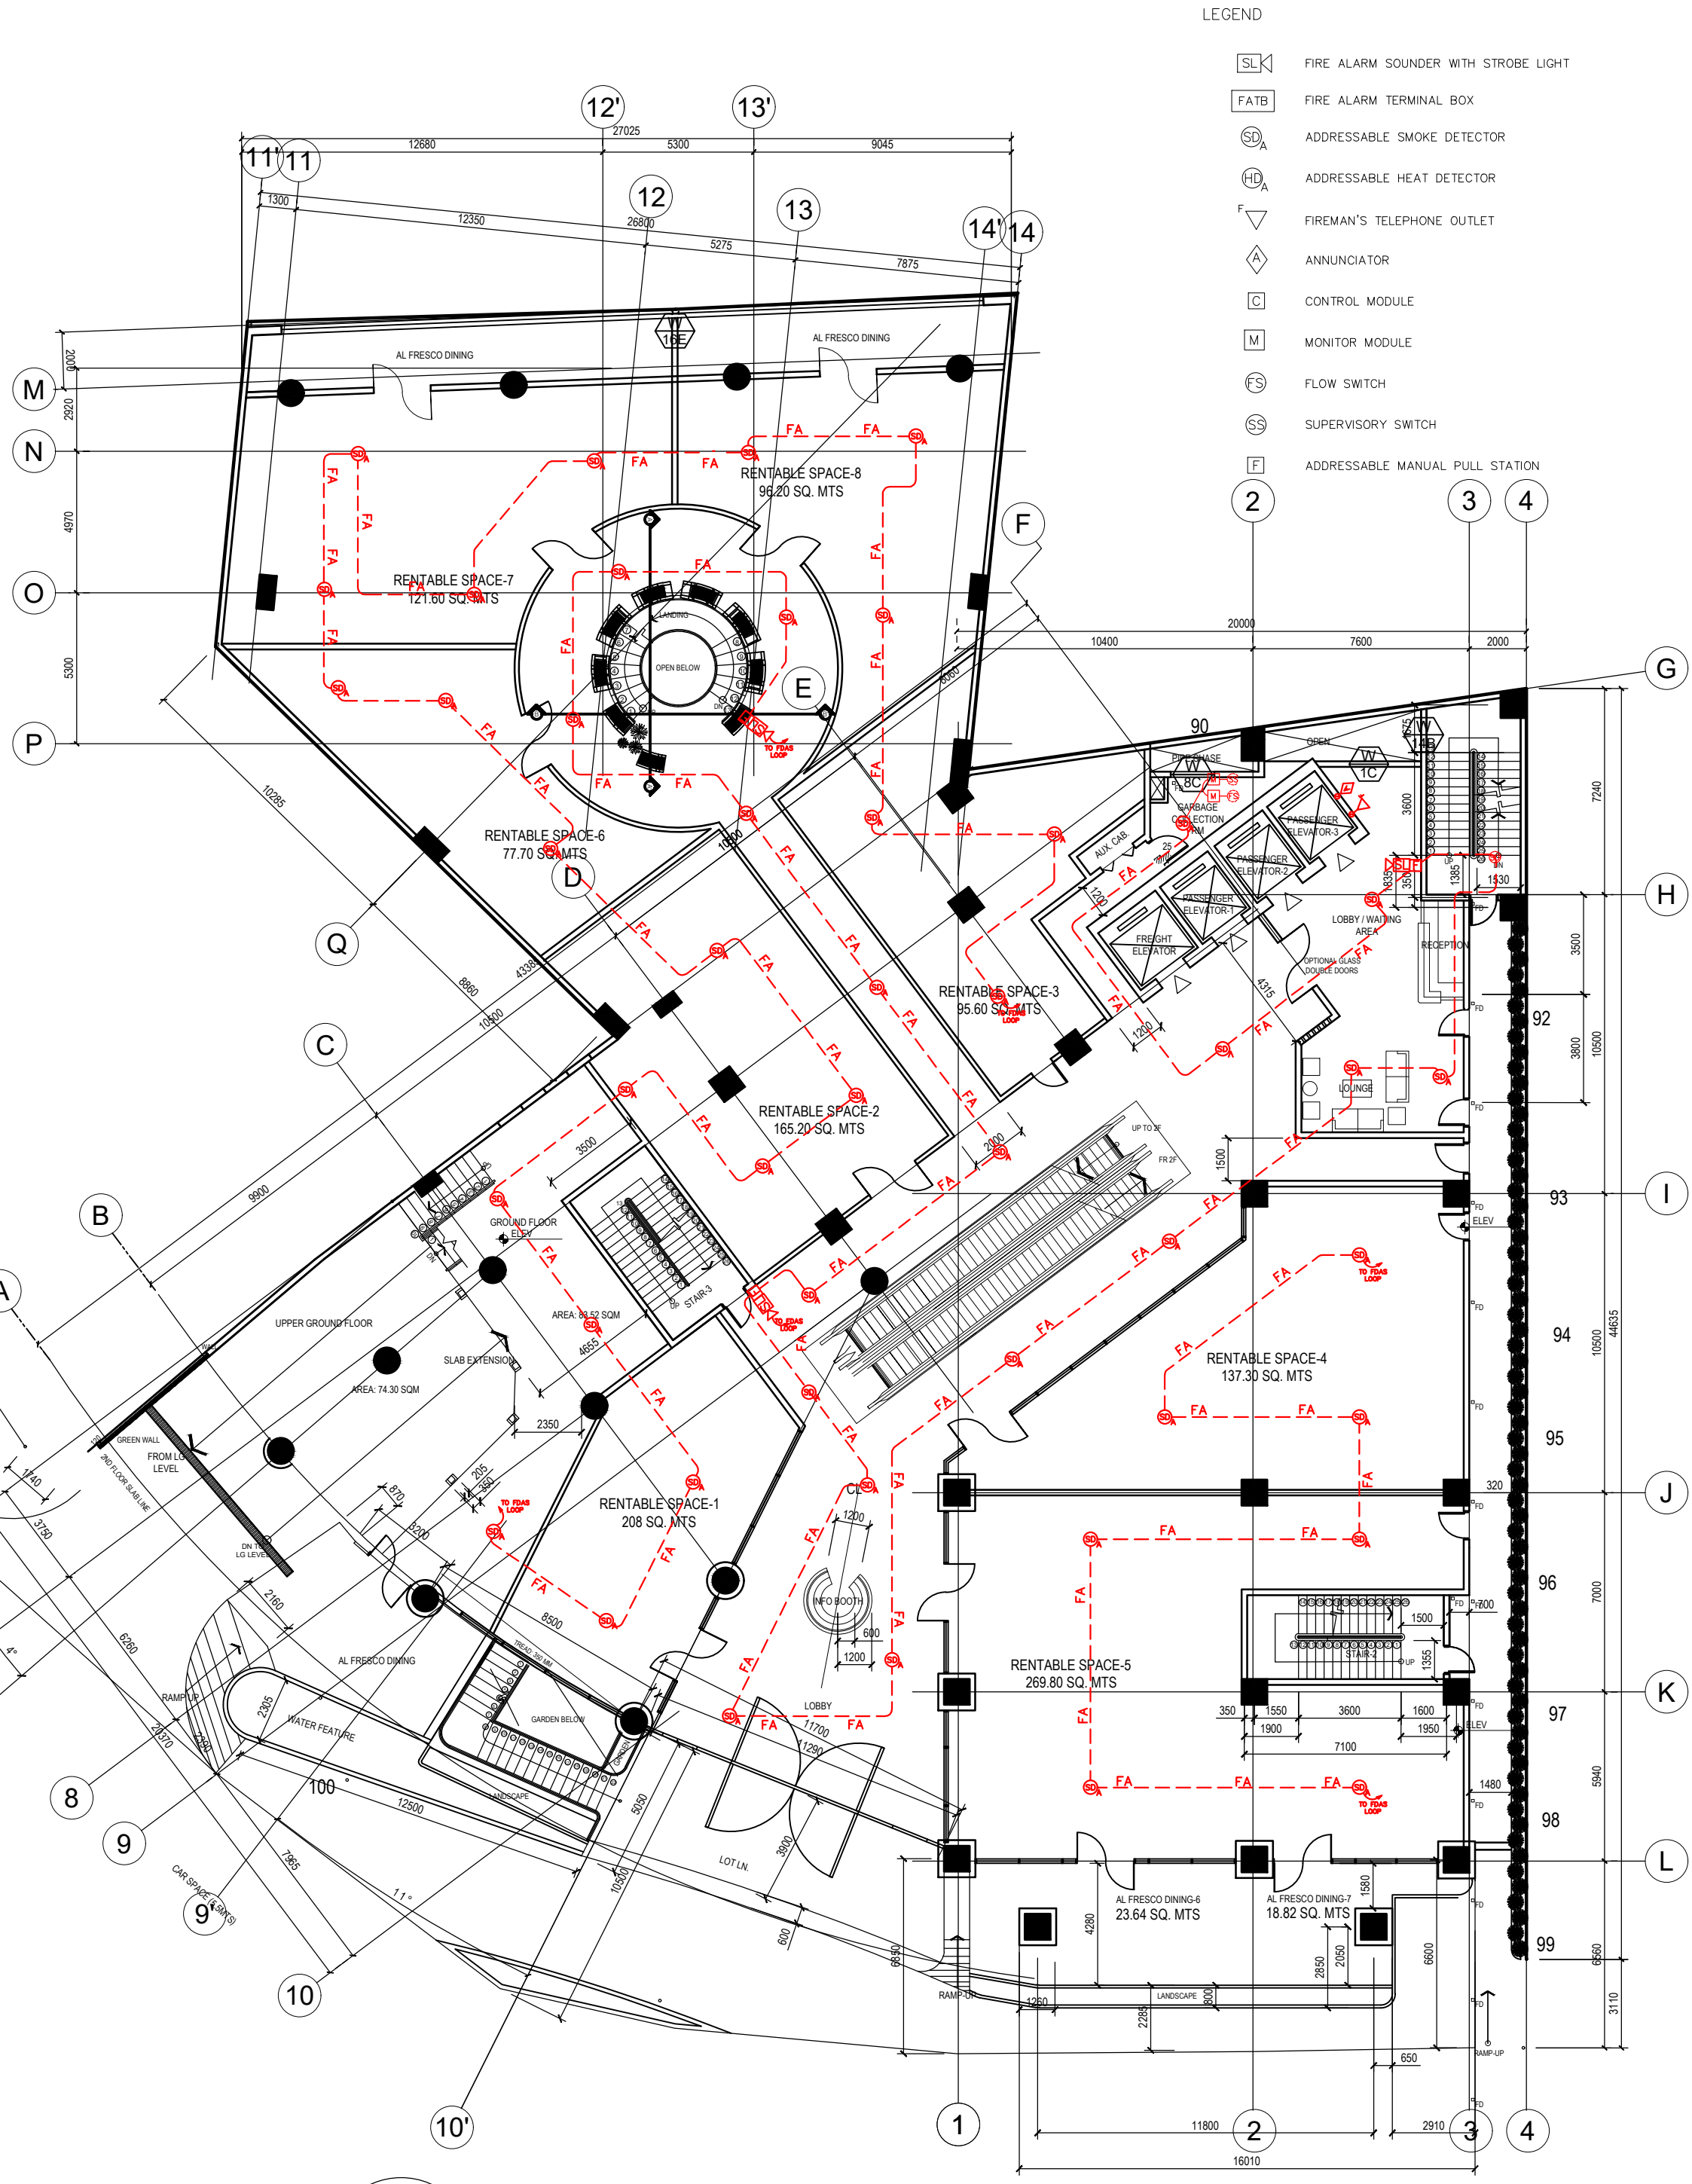

1 GROUND FLOOR FDAS LAYOUT

07

SCALE **1:200M**

LEGEND

SL	FIRE ALARM SOUNDER WITH STROBE LIGHT
FATB	FIRE ALARM TERMINAL BOX
SD A	ADDRESSABLE SMOKE DETECTOR
HD A	ADDRESSABLE HEAT DETECTOR
F	FIREMAN'S TELEPHONE OUTLET
A	ANNUNCIATOR
C	CONTROL MODULE
M	MONITOR MODULE
FS	FLOW SWITCH
SS	SUPERVISORY SWITCH
F	ADDRESSABLE MANUAL PULL STATION

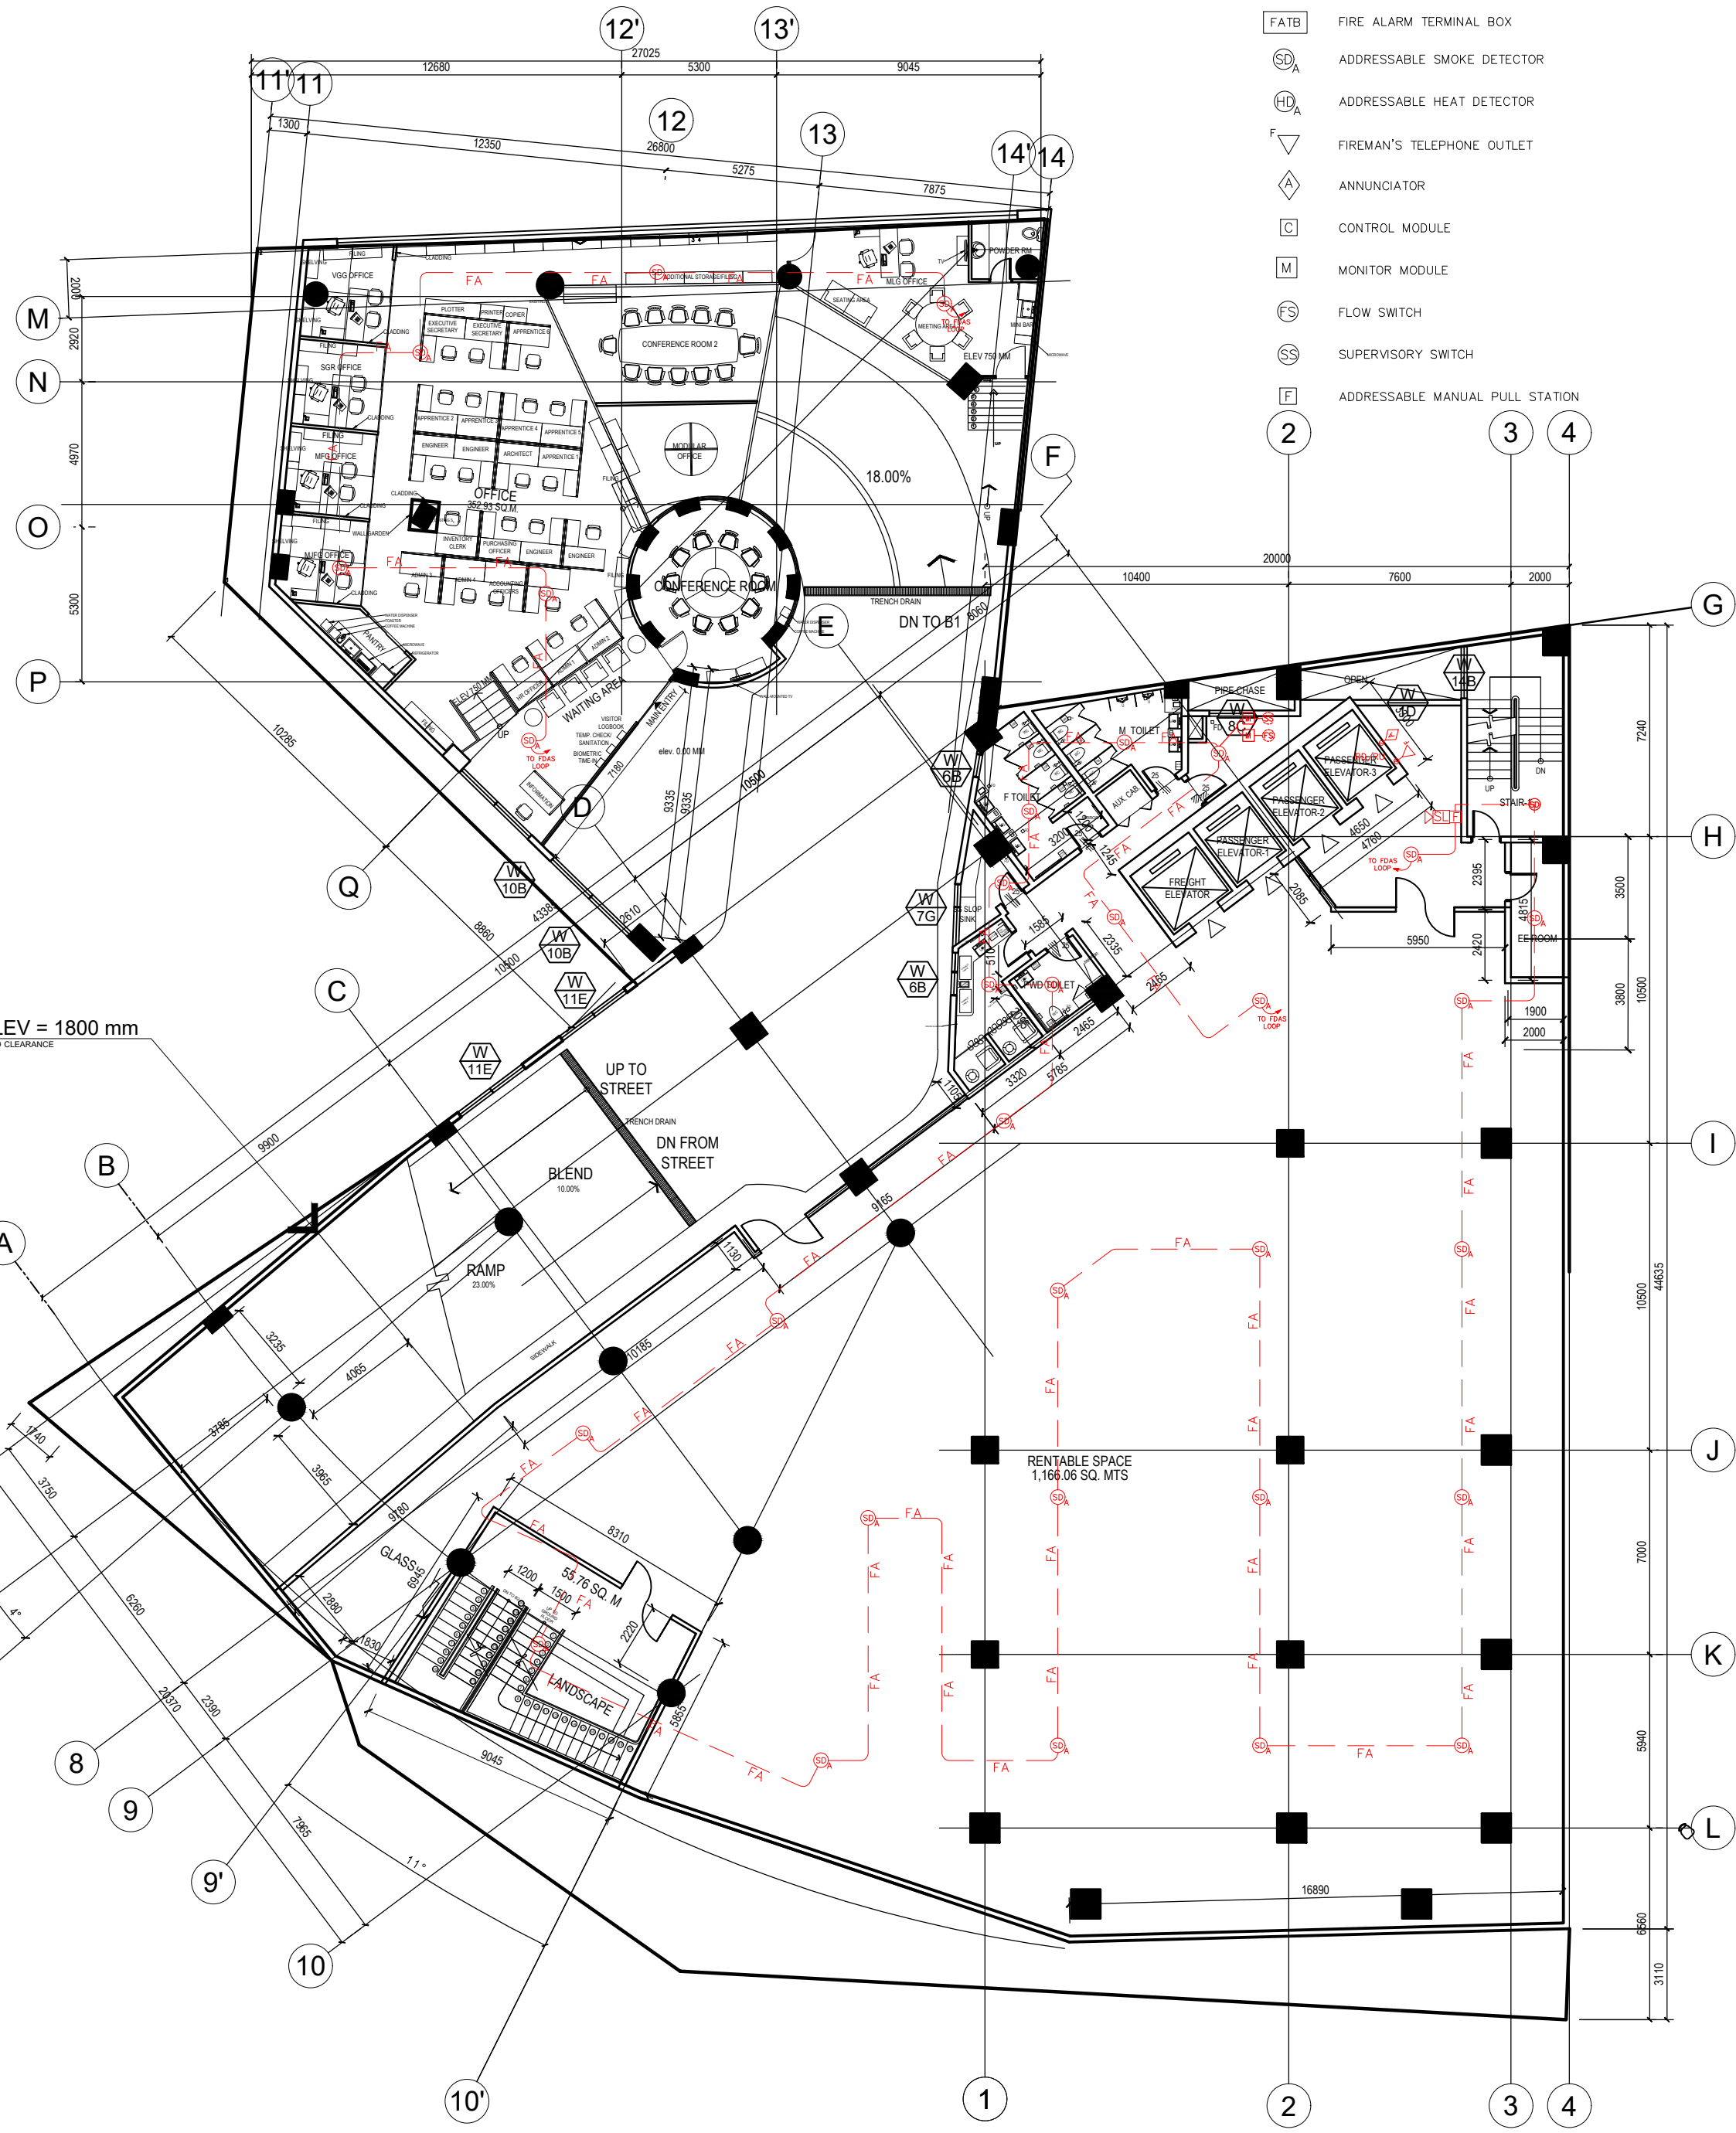

1 LOWER GROUND FDAS LAYOUT

06

SCALE 1:200M

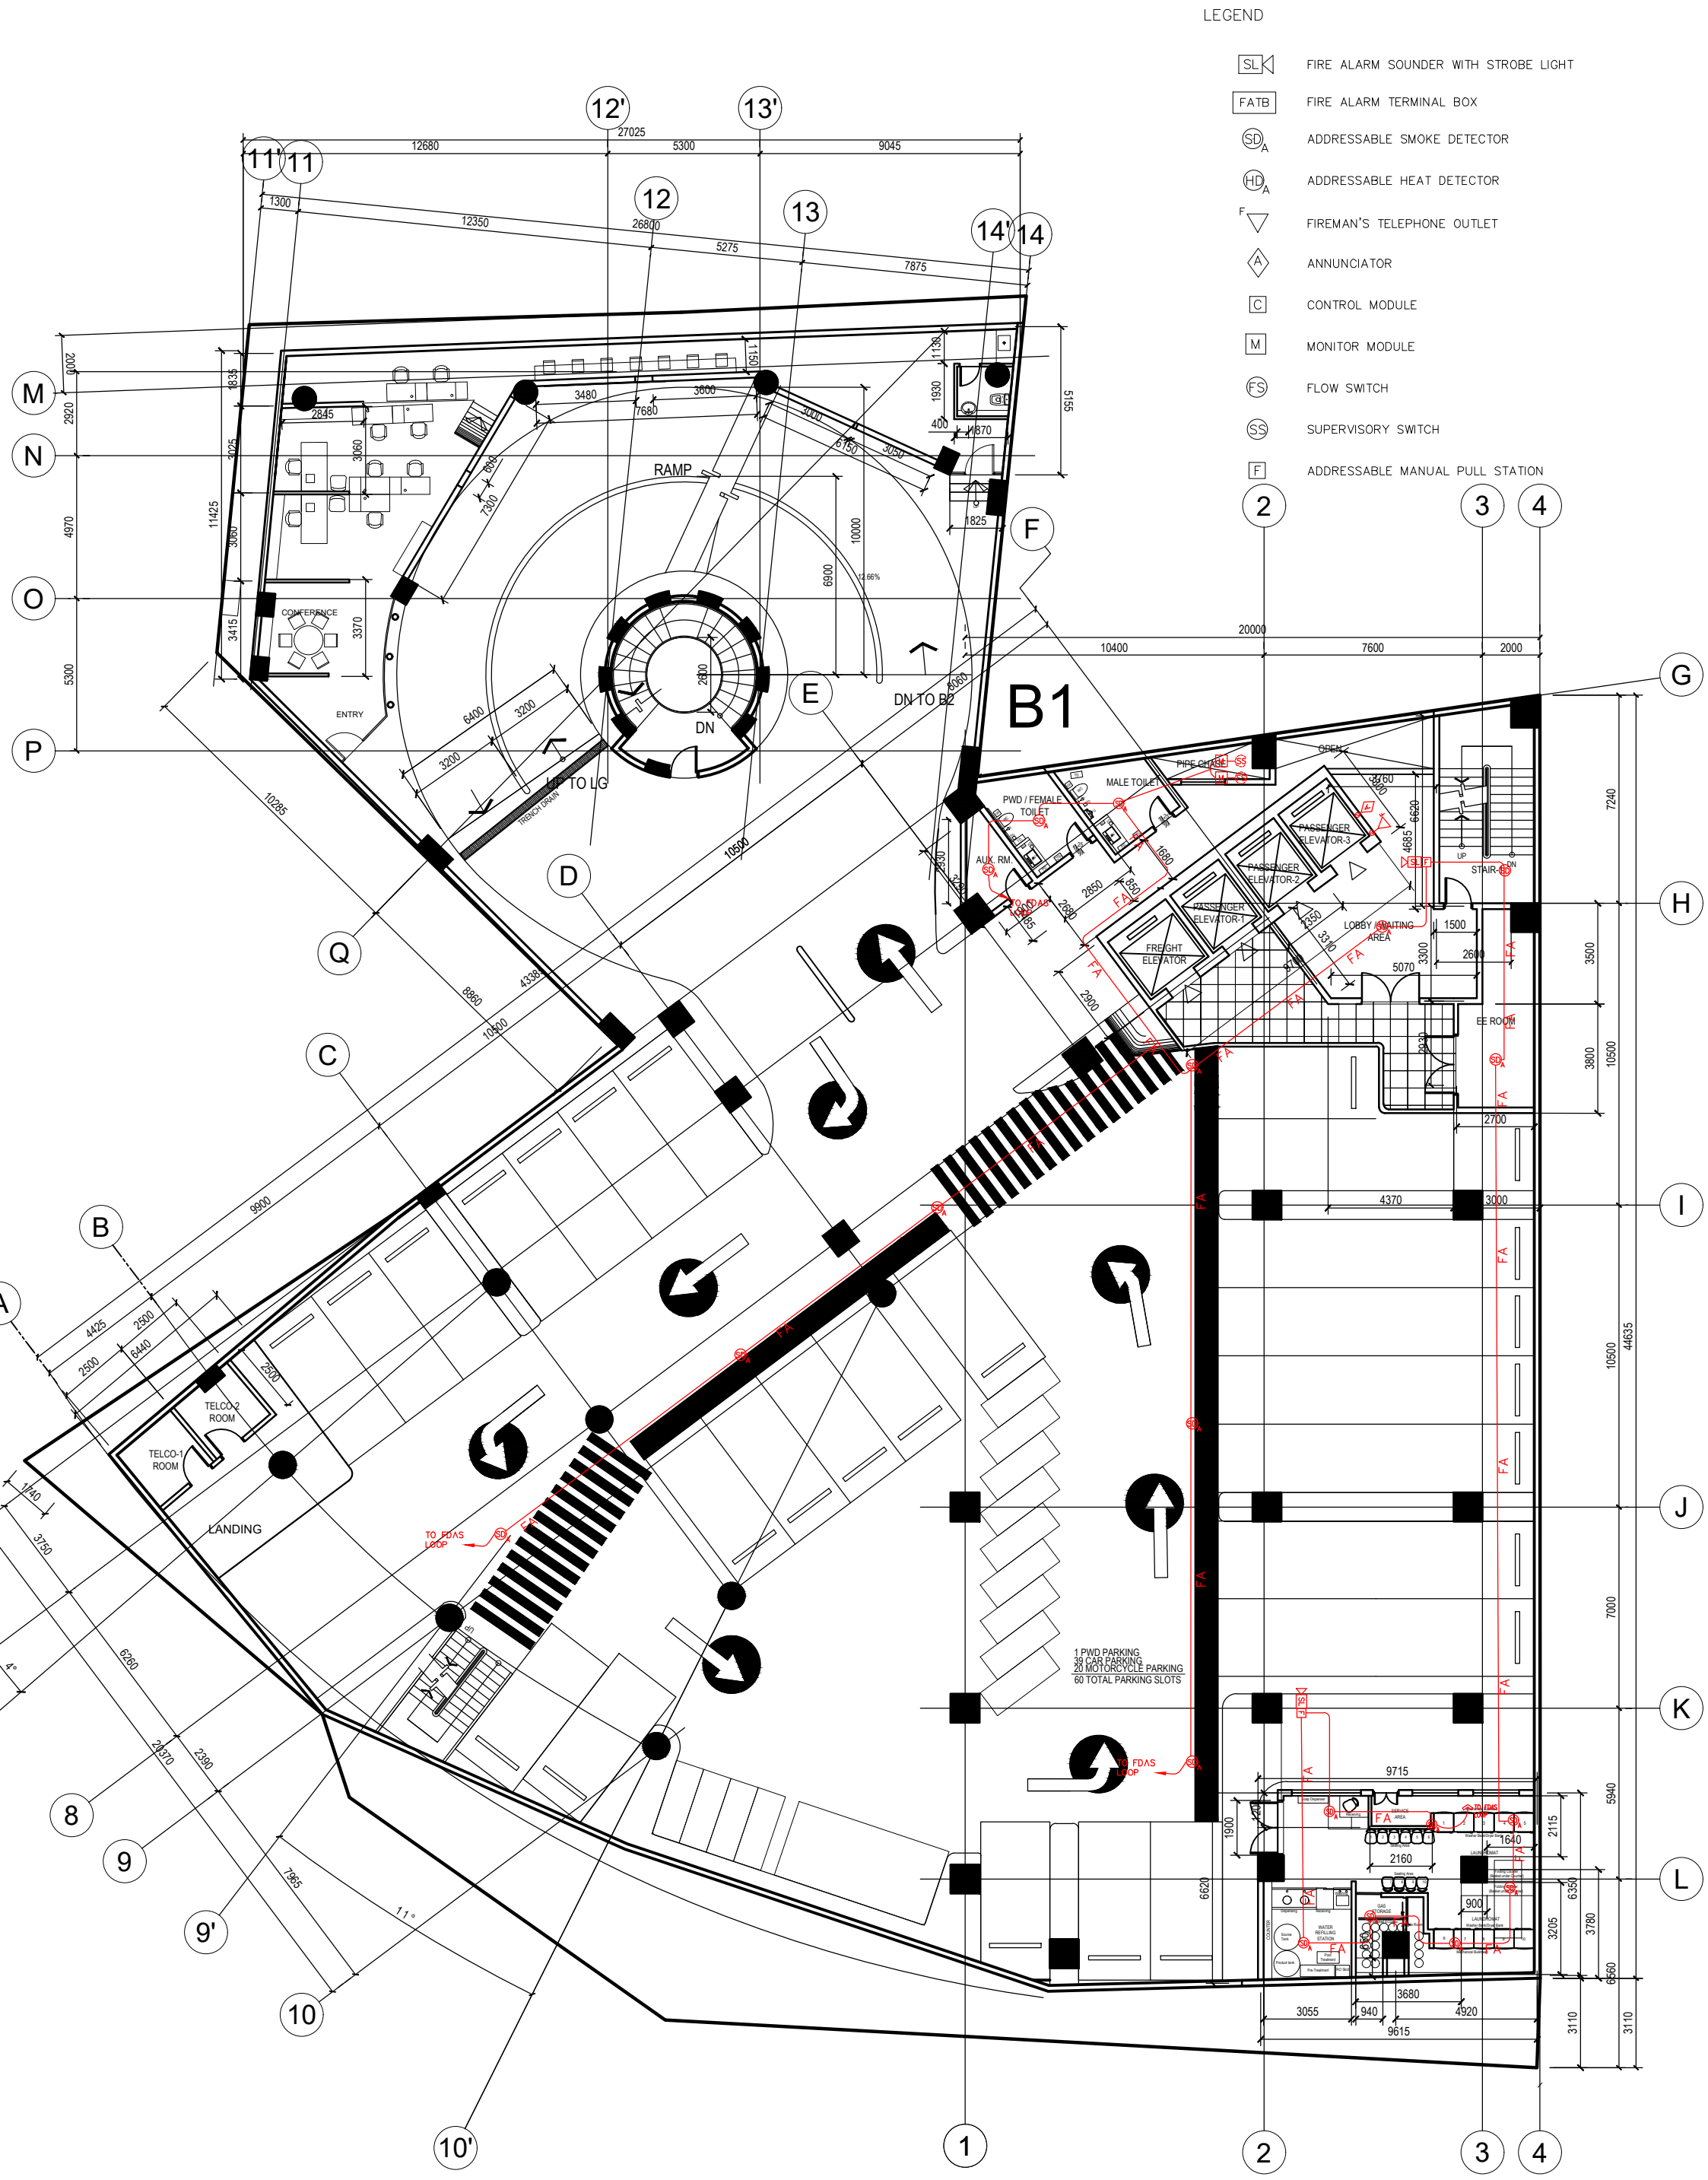

1 LOWER GROUND 1 FDAS LAYOUT

05

SCALE 1:200M

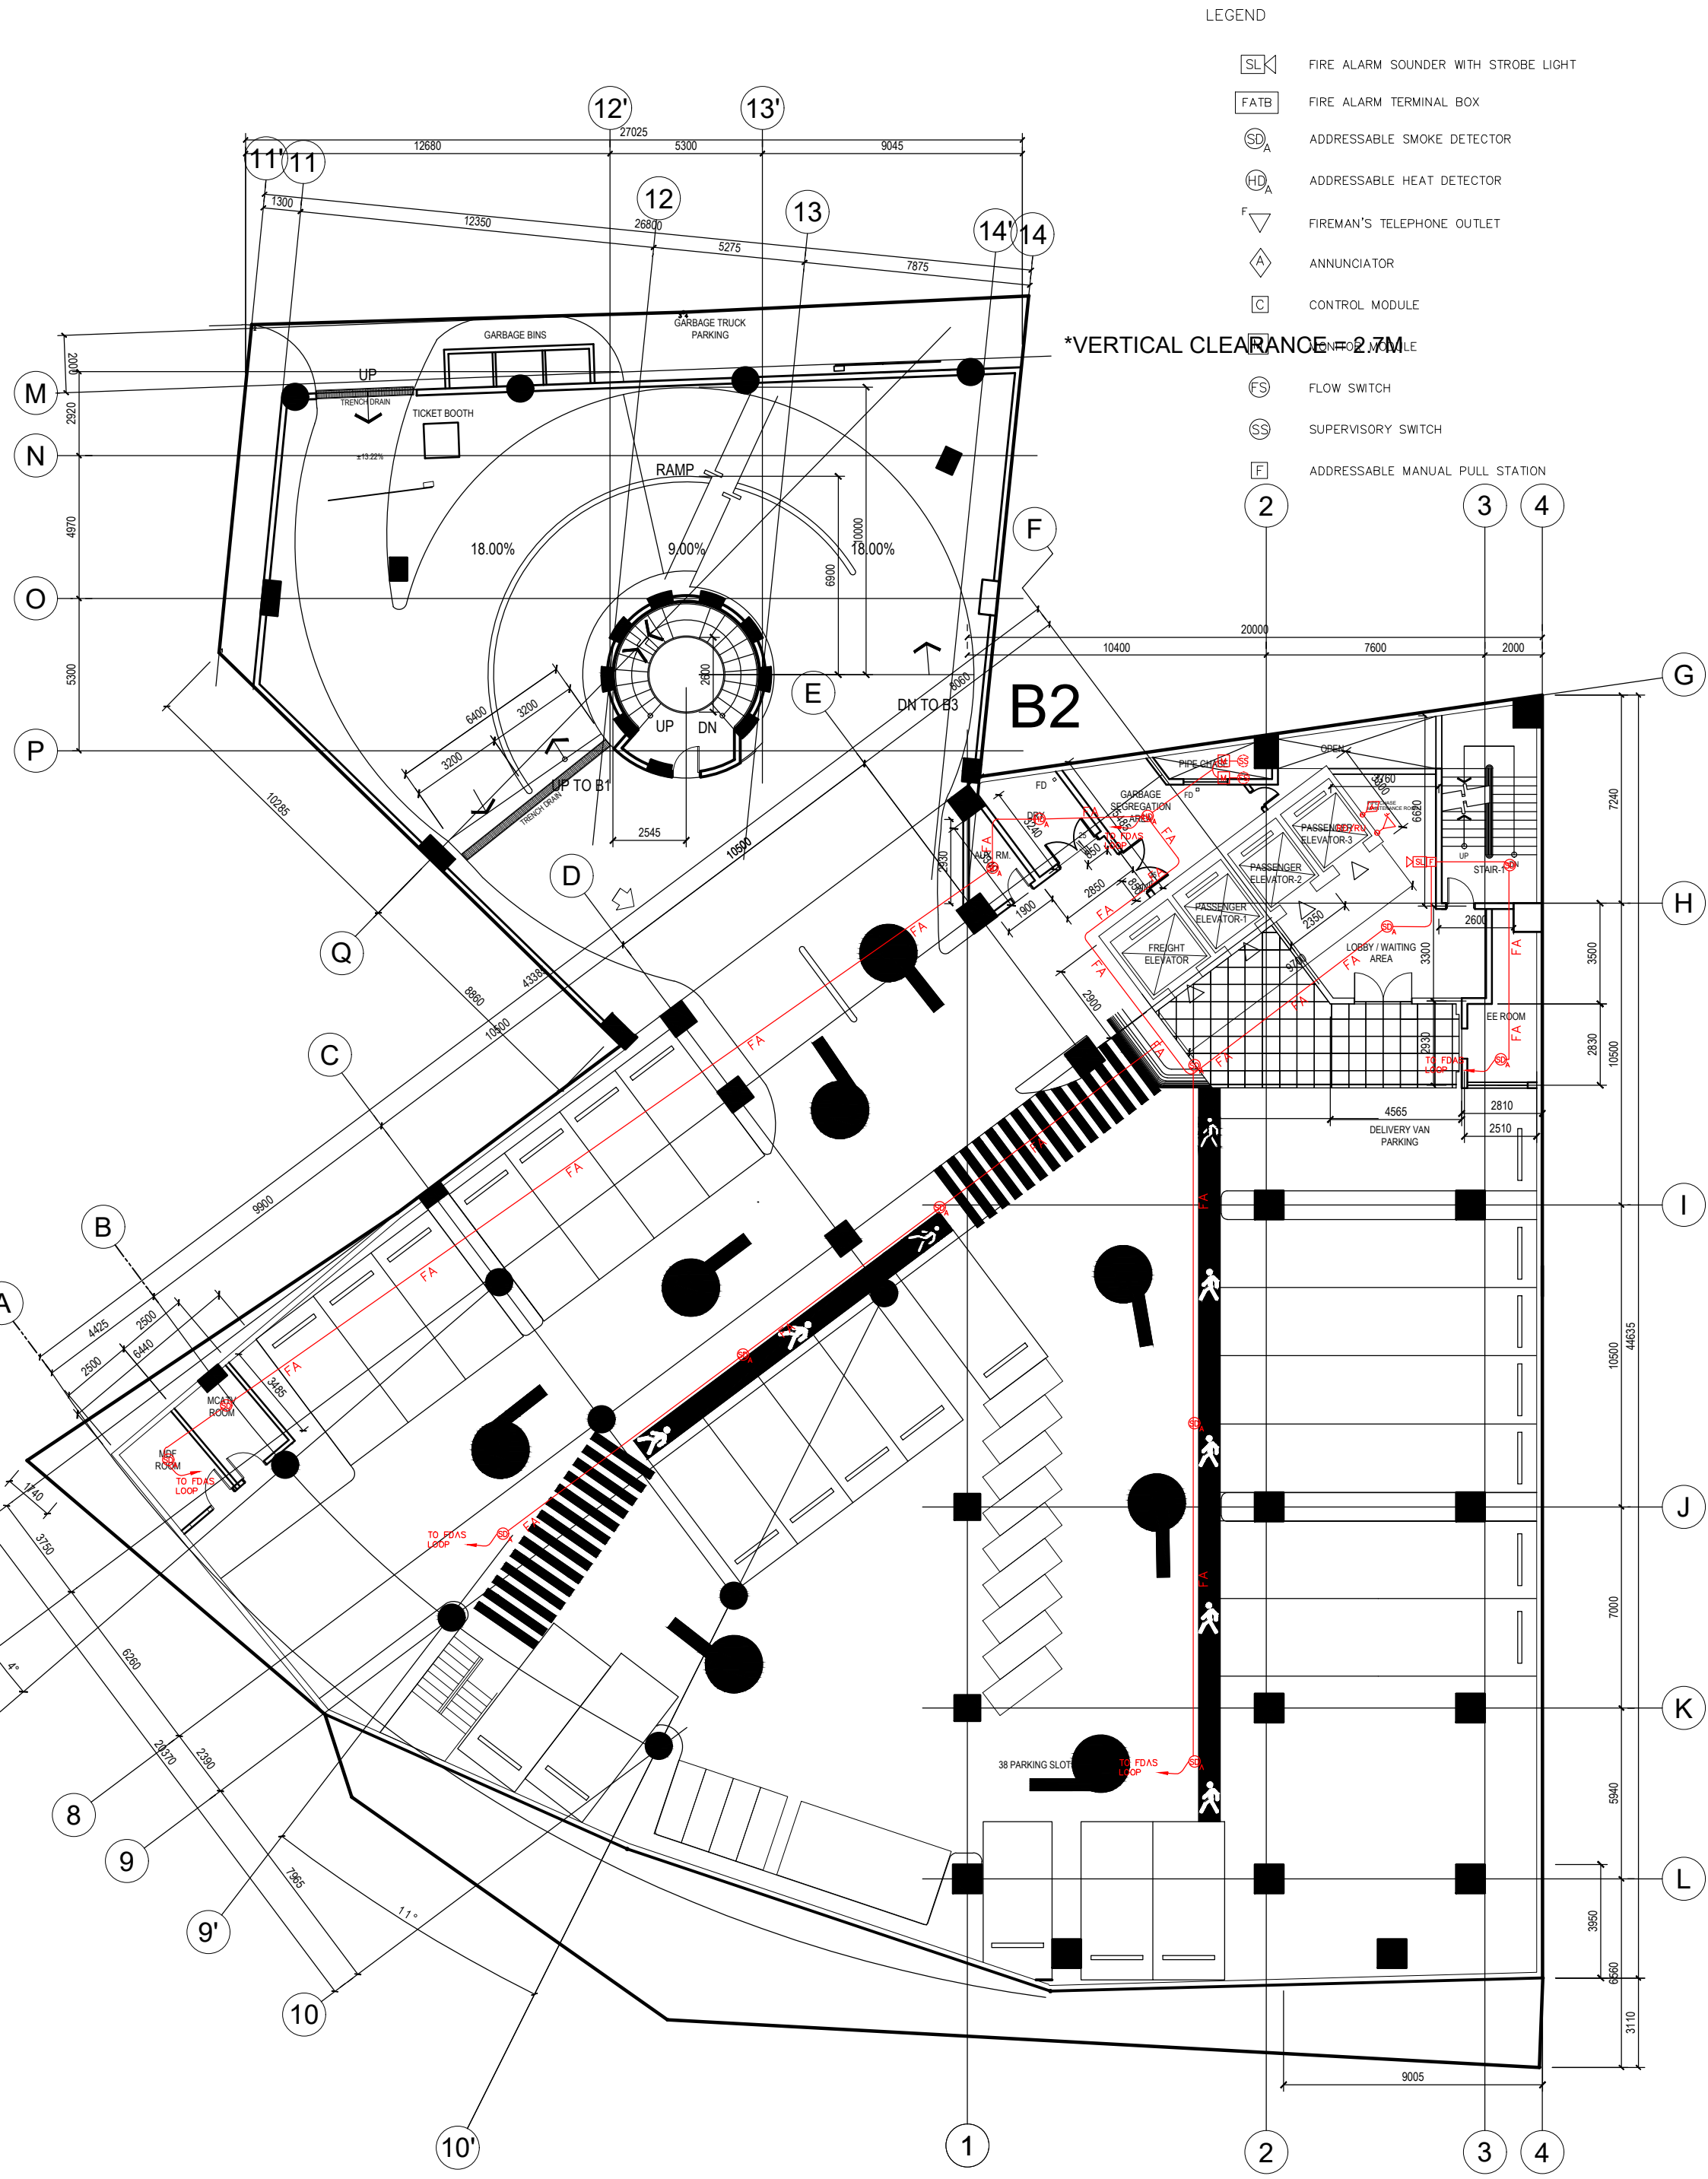

1 LOWER GROUND 2 FDAS LAYOUT

04

SCALE 1:200M

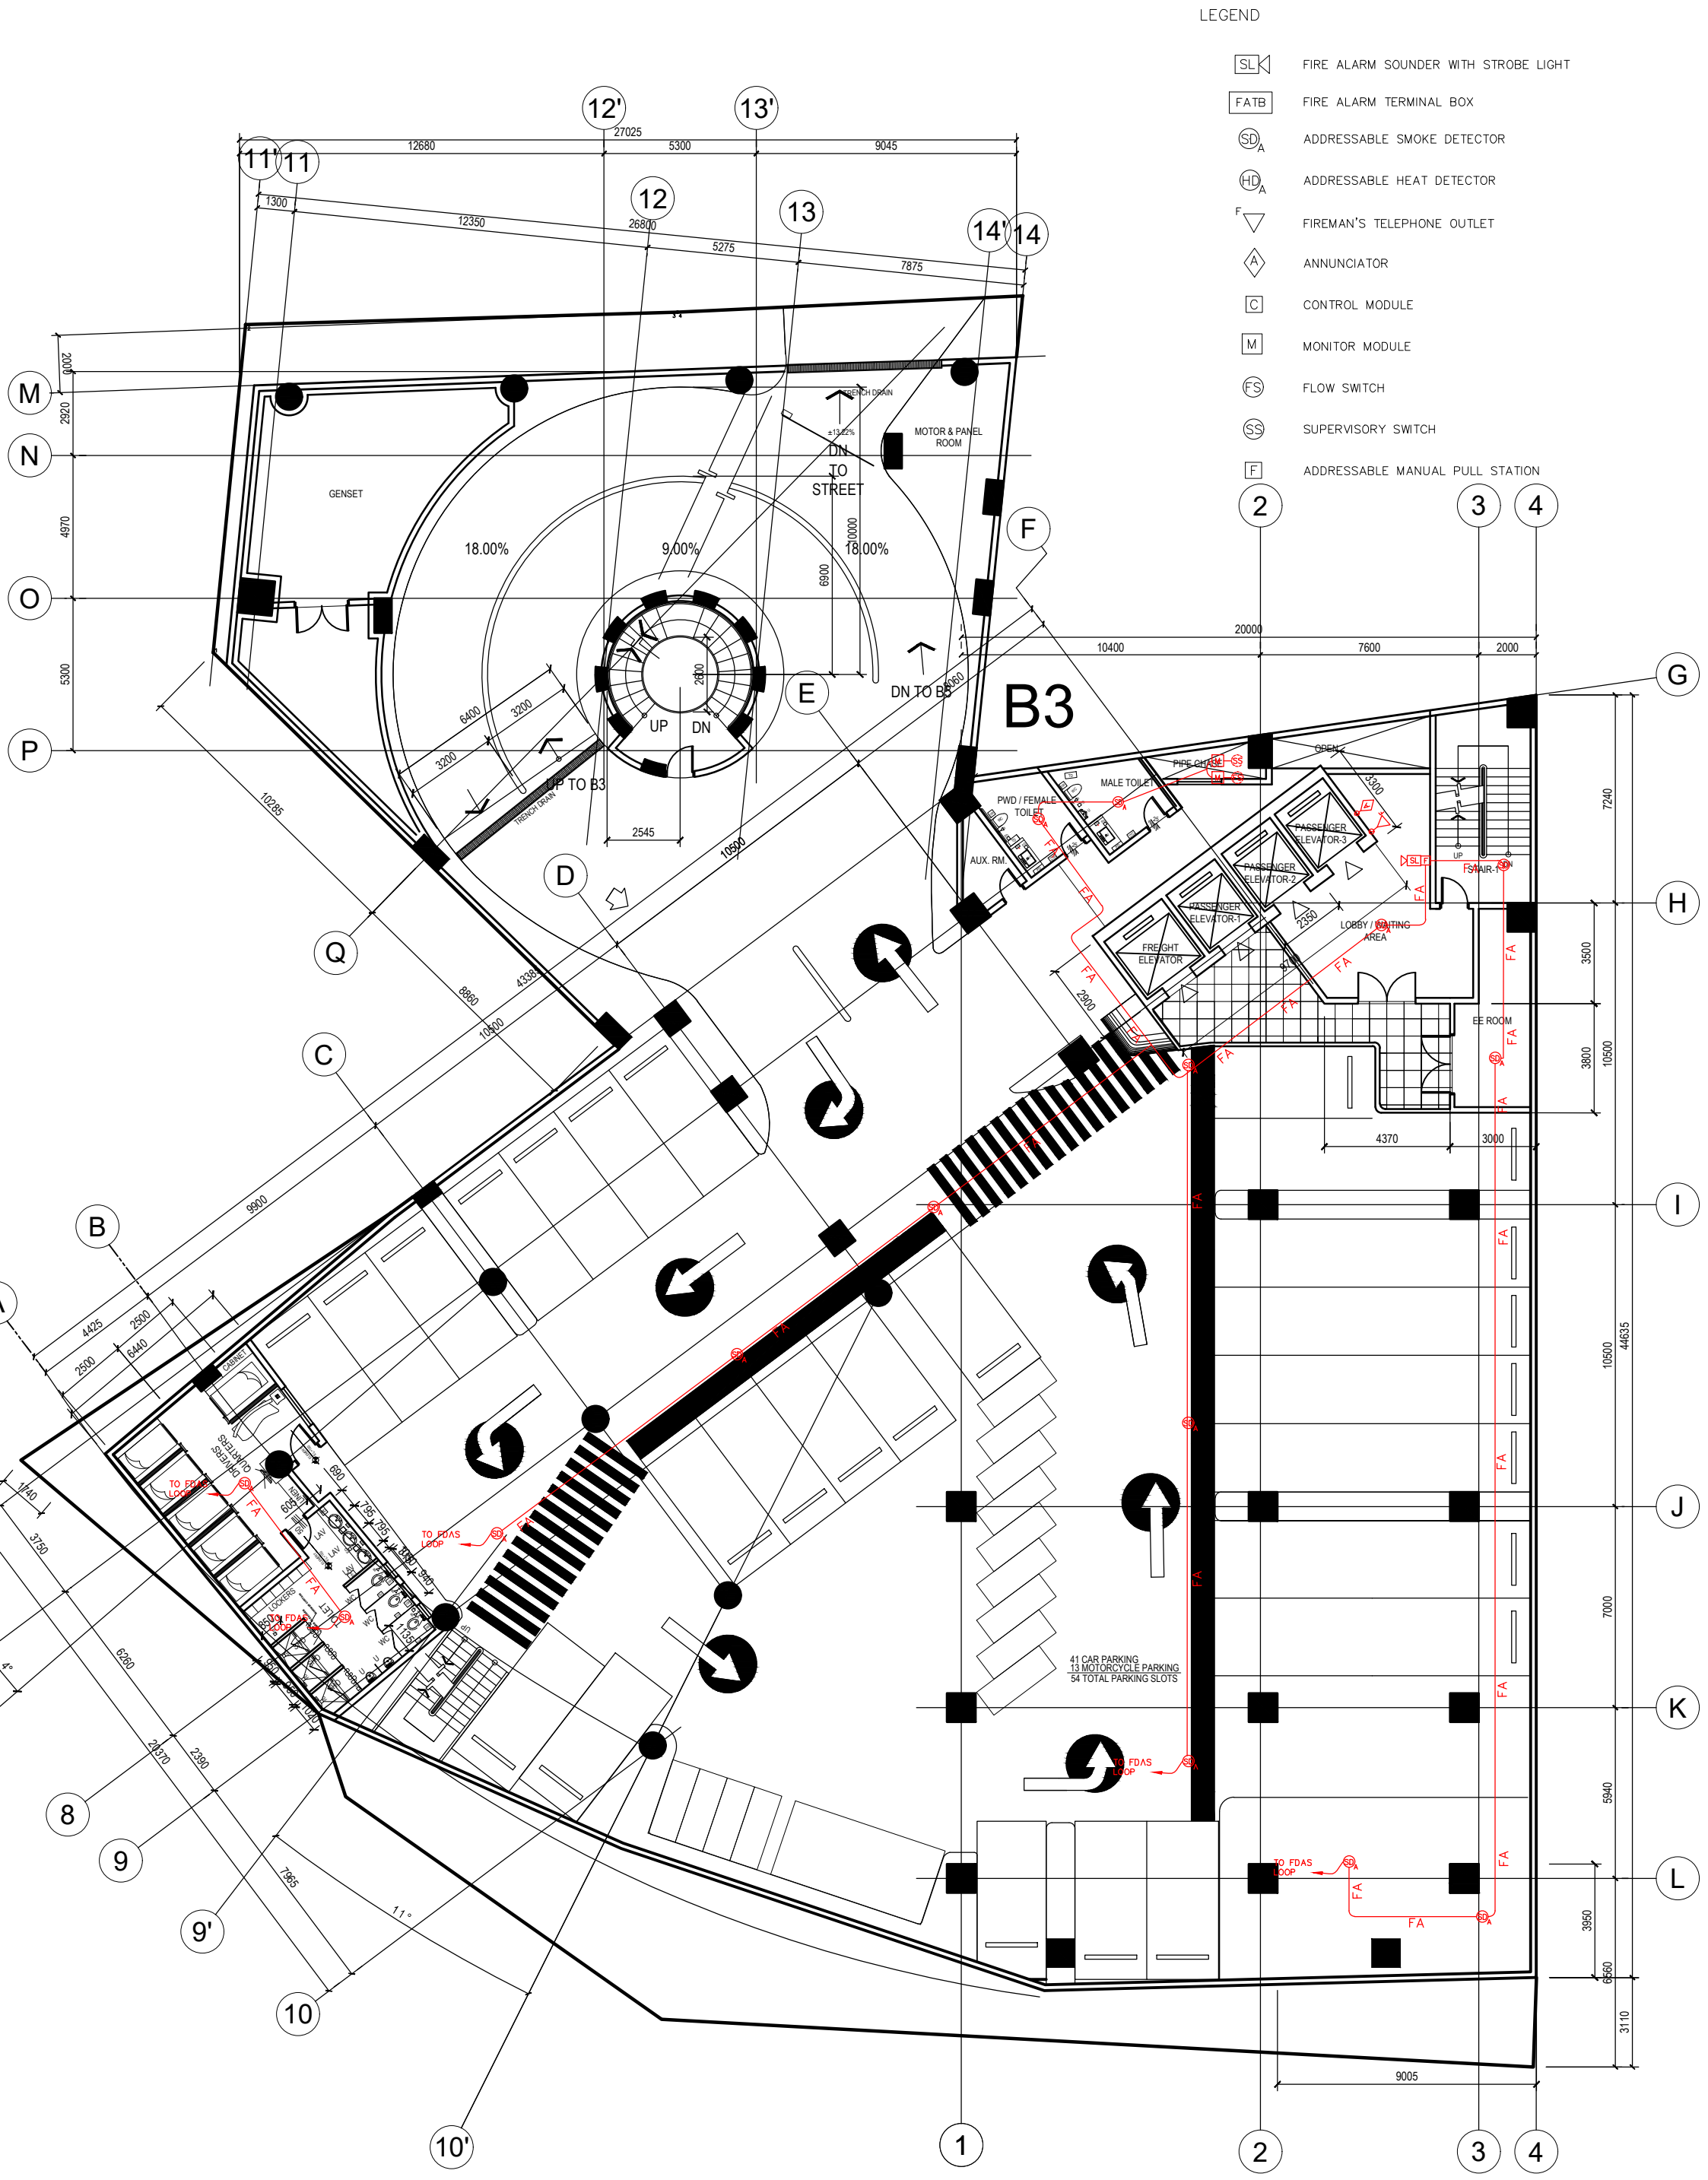

1 LOWER GROUND 3 FDAS LAYOUT

03

SCALE 1:200M